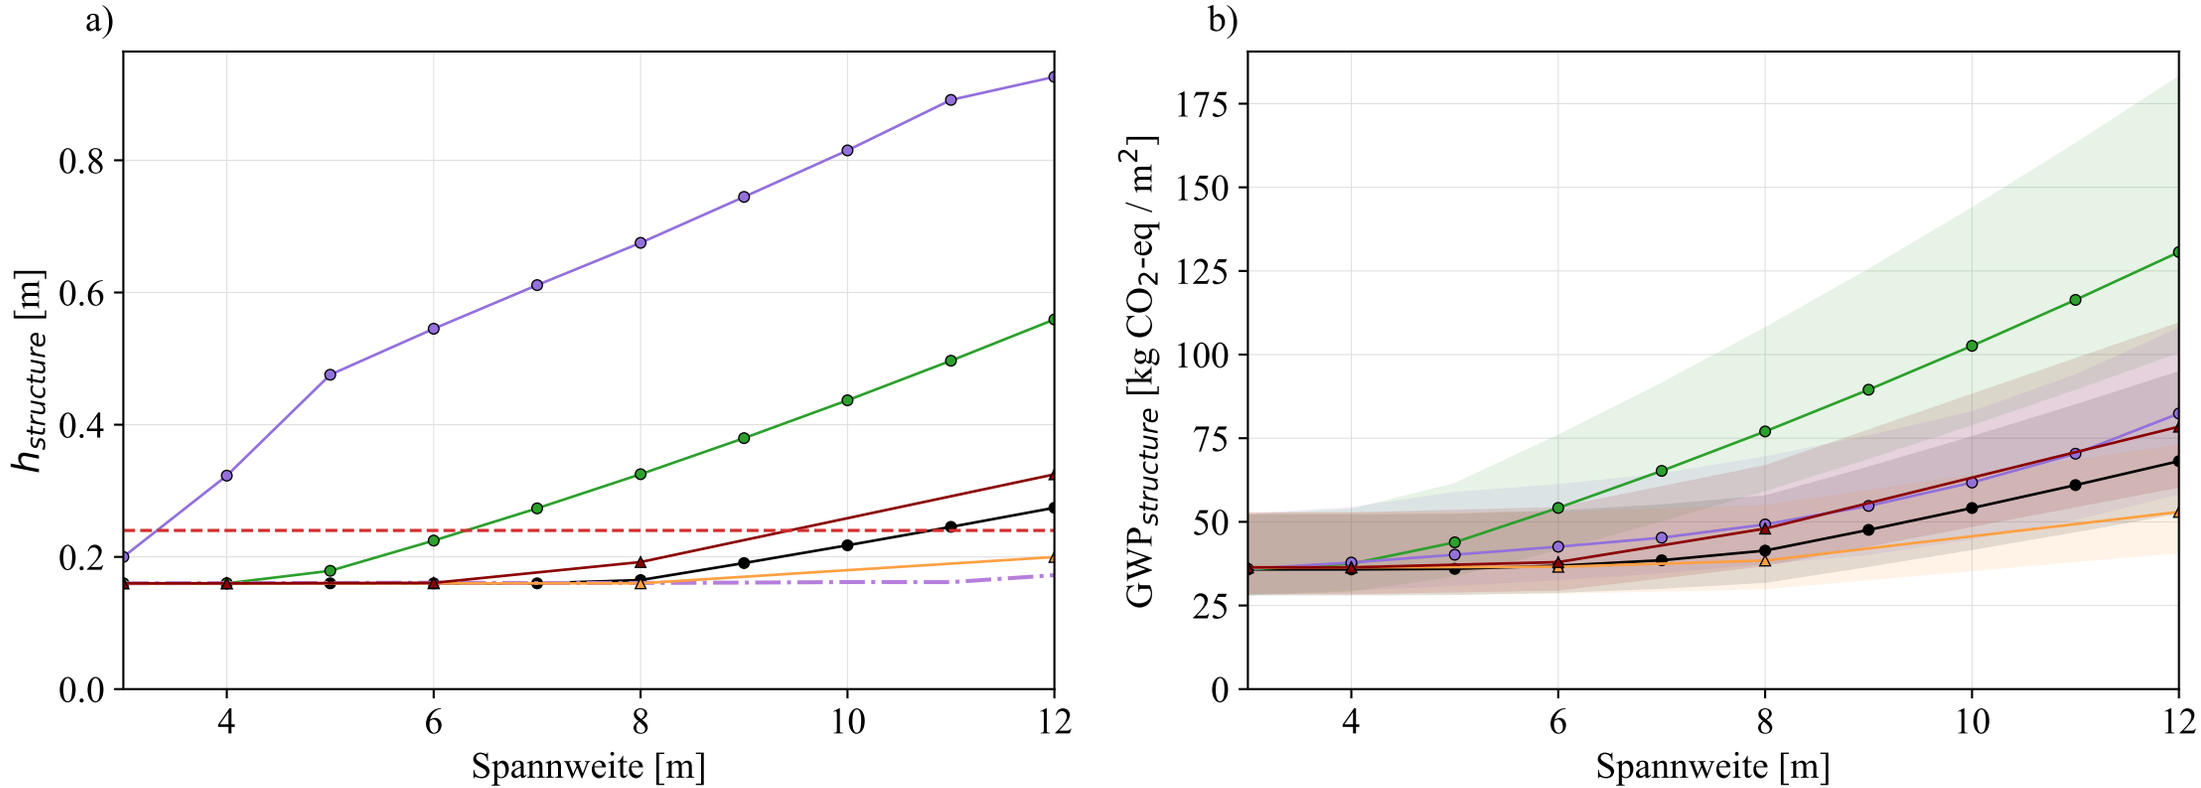

Vollplatte, einachsig tragend, einfach gelagert (Standardaufbau)

Vollplatte, einachsig tragend, durchlaufend (Standardaufbau)

Mindeststärke für erhöhte Schallschutzanforderungen (24 cm)

Vollplatte, zweiachsig tragend, einfach gelagert (Standardaufbau)

Vollplatte, zweiachsig tragend, durchlaufend (Standardaufbau)

Rippenplatte, einachsig tragend, einfach gelagert (Standardaufbau)

Rippenplatte, einachsig tragend, einfach gelagert (Standardaufbau), Flanschhöhe