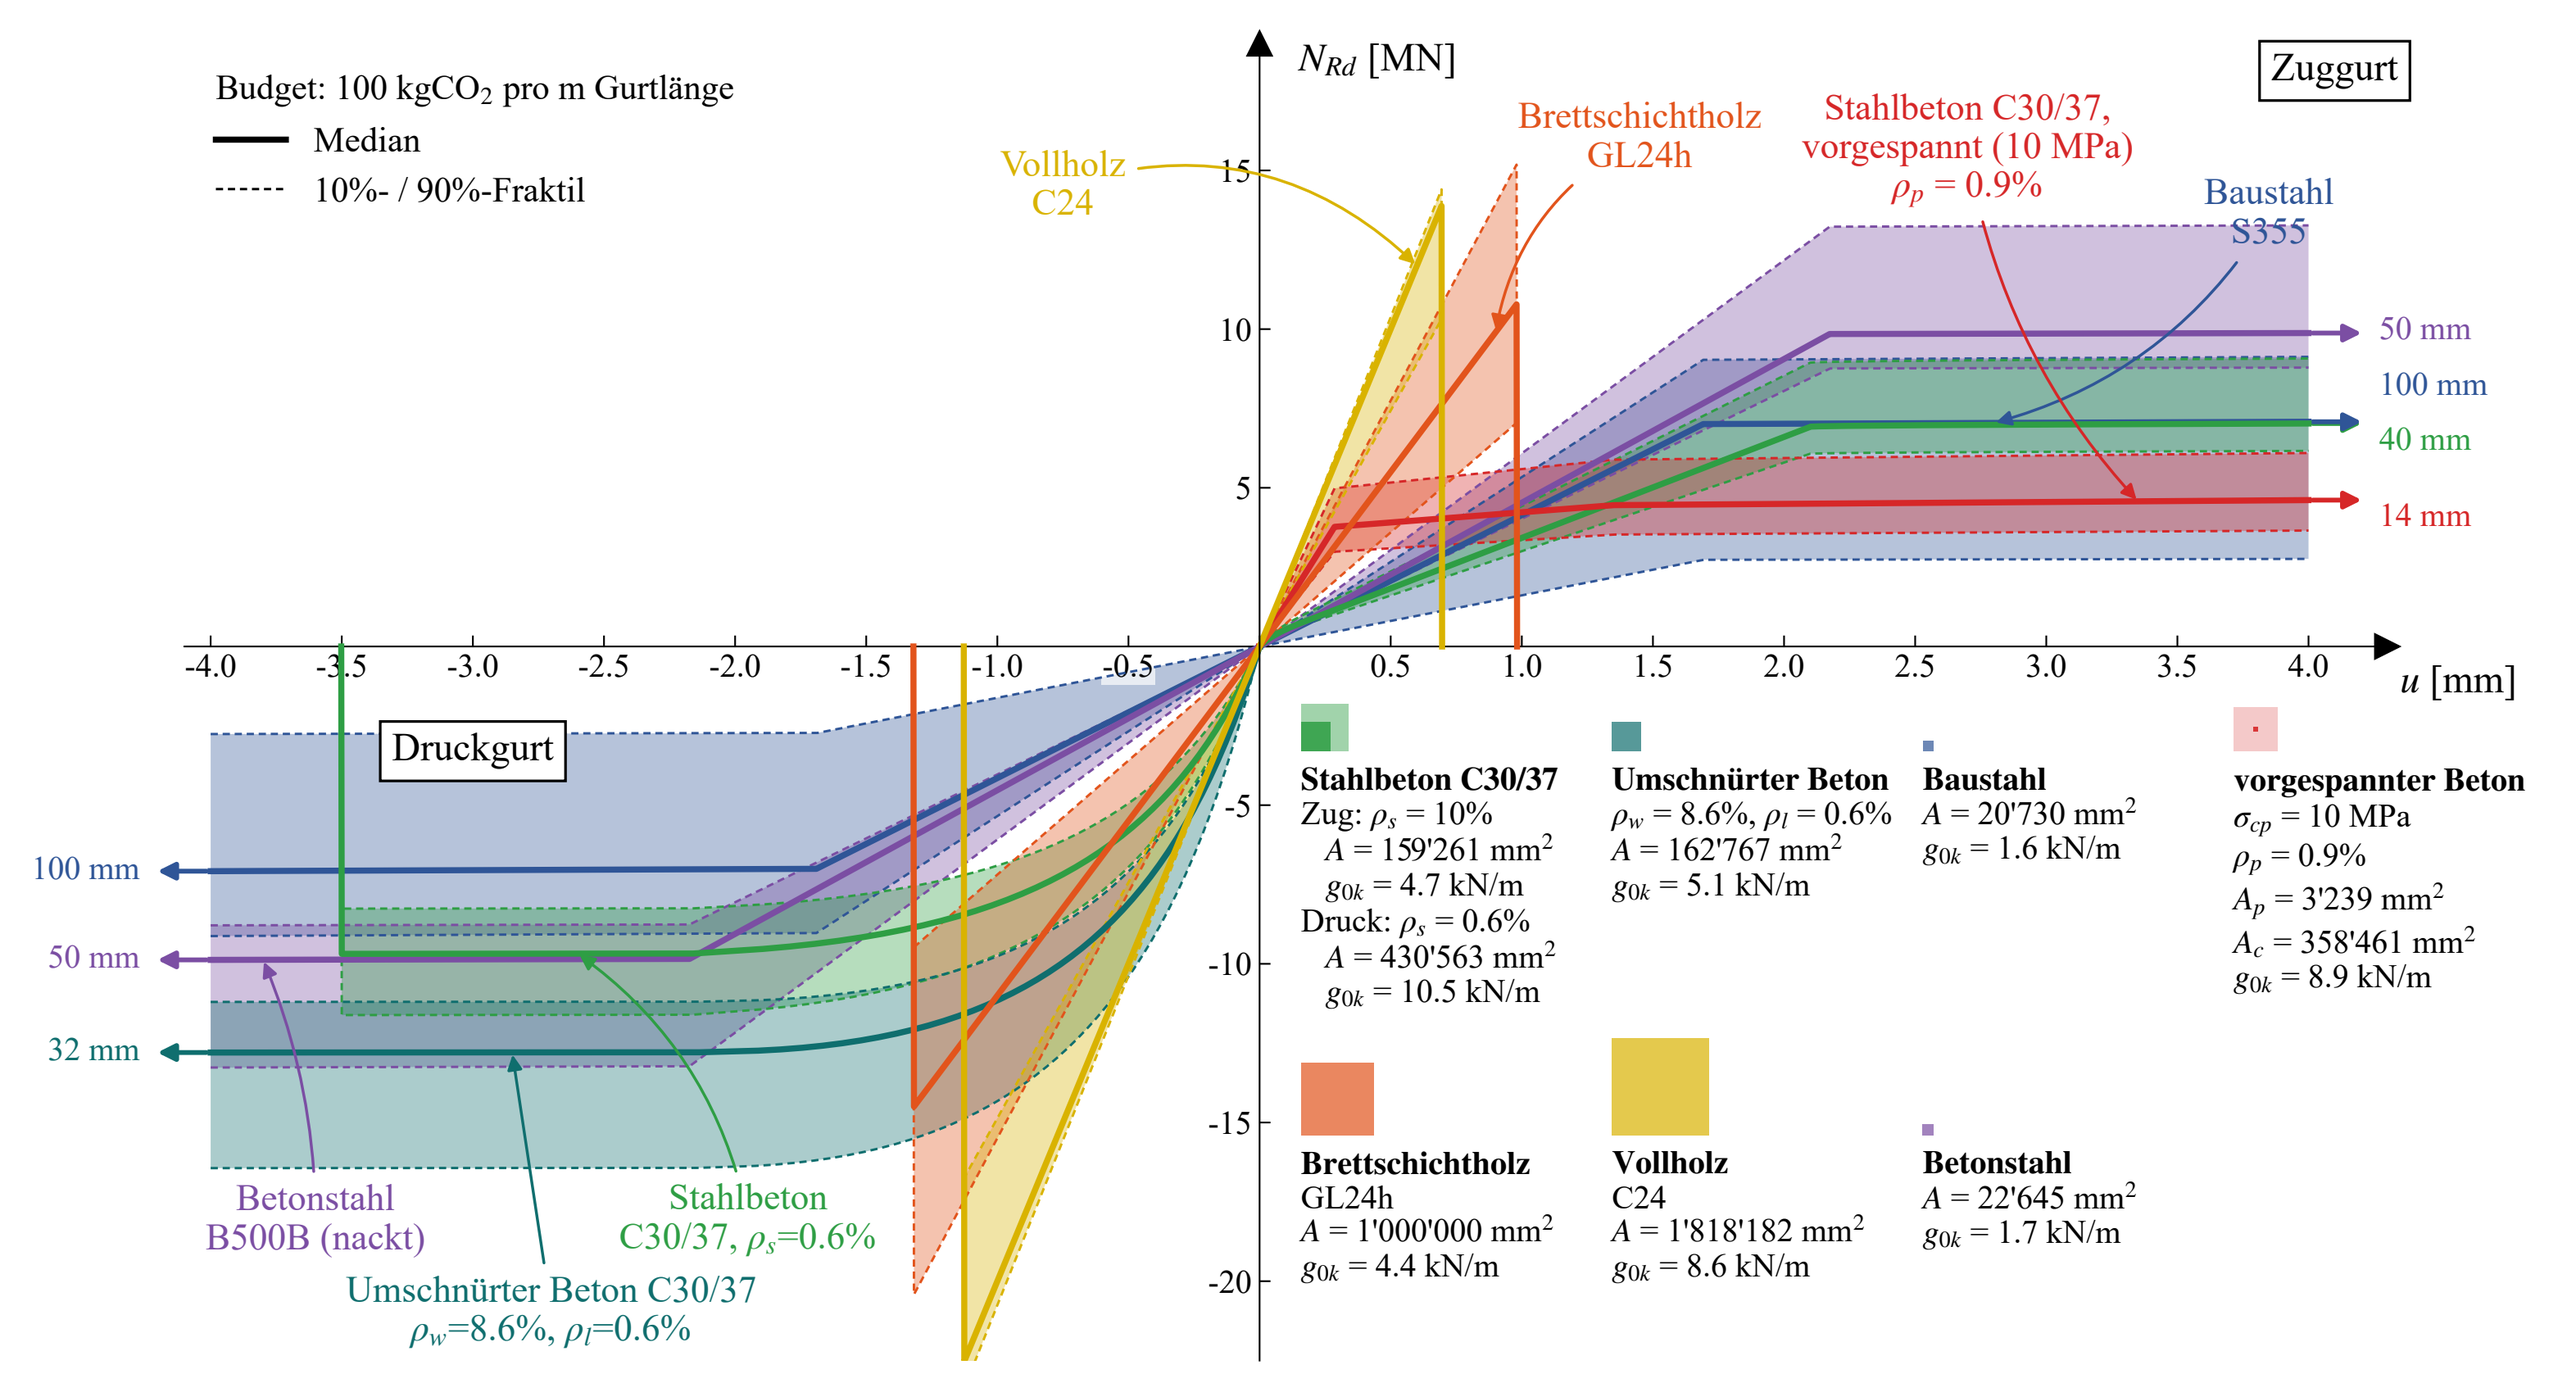

Budget: 100 kgCO2 pro m Gurtlänge
Median
10%- / 90%-Fraktil
NRd [MN]
Zuggurt
Vollholz C24
Brettschichtholz GL24h
Stahlbeton C30/37, vorgespannt (10 MPa) ρp = 0.9%
Baustahl S355
50 mm
100 mm
40 mm
14 mm
u [mm]
Druckgurt
100 mm
50 mm
32 mm
Betonstahl B500B (nackt)
Stahlbeton C30/37, ρs=0.6%
Umschnürter Beton C30/37 ρw=8.6%, ρl=0.6%
Stahlbeton C30/37
Zug: ρs = 10%
A = 159'261 mm2
g0k = 4.7 kN/m
Druck: ρs = 0.6%
A = 430'563 mm2
g0k = 10.5 kN/m
Umschnürter Beton
ρw = 8.6%, ρl = 0.6%
A = 162'767 mm2
g0k = 5.1 kN/m
Baustahl
A = 20'730 mm2
g0k = 1.6 kN/m
vorgespannter Beton
σcp = 10 MPa
ρp = 0.9%
Ap = 3'239 mm2
Ac = 358'461 mm2
g0k = 8.9 kN/m
Brettschichtholz
GL24h
A = 1'000'000 mm2
g0k = 4.4 kN/m
Vollholz
C24
A = 1'818'182 mm2
g0k = 8.6 kN/m
Betonstahl
A = 22'645 mm2
g0k = 1.7 kN/m