
(a)

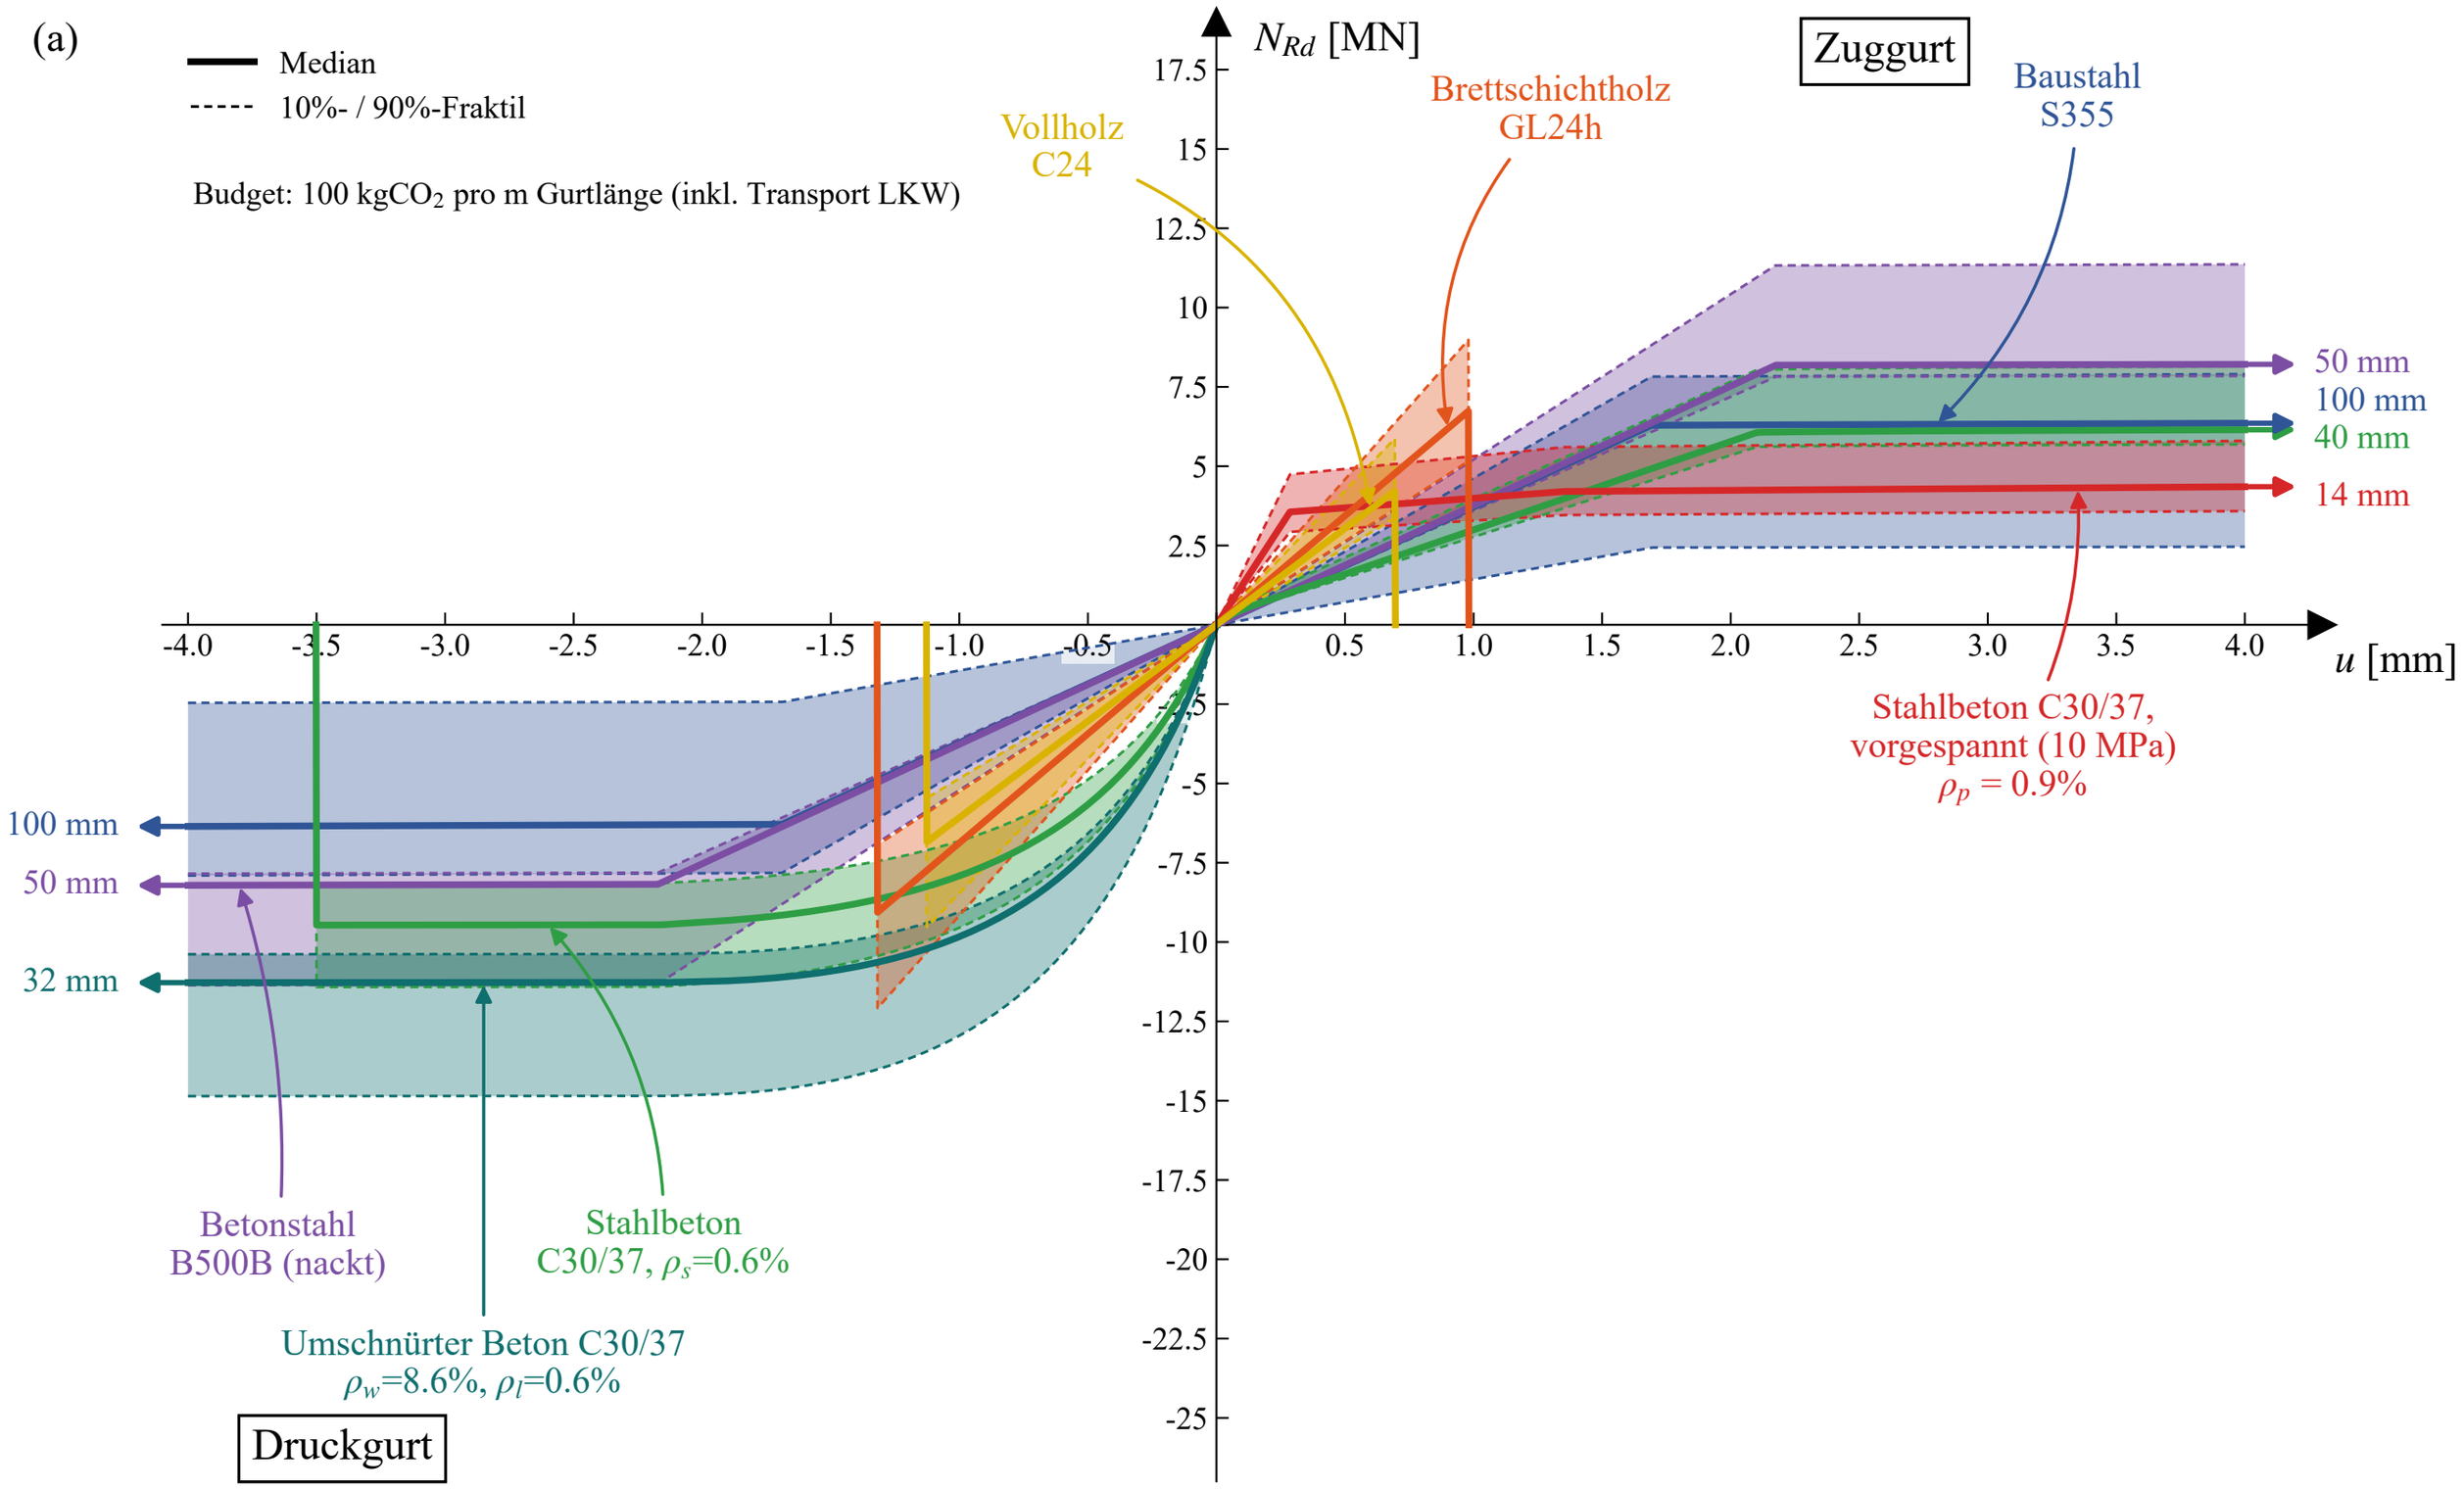

(b)



vorgespannter Beton
σ_{cp} = 10 MPa
ρ_p = 0.9%
A_p = 3'057 mm^2
A_c = 338'330 mm^2
g_{0k} = 8.4 kN/m

Baustahl
A = 18'605 mm^2
g_{0k} = 1.4 kN/m

Betonstahl
A = 18'829 mm^2
g_{0k} = 1.4 kN/m

Stahlbeton C30/37
Zug: ρ_s = 10%
A = 139'392 mm^2
g_{0k} = 4.1 kN/m
Druck: ρ_s = 0.6%
A = 420'833 mm^2
g_{0k} = 10.2 kN/m

Umschnürter Beton
ρ_w = 8.6%, ρ_l = 0.6%
A = 143'484 mm^2
g_{0k} = 4.5 kN/m

Brettschichtholz
GL24h
A = 625'000 mm^2
g_{0k} = 2.8 kN/m

Vollholz
C24
A = 552'486 mm^2
g_{0k} = 2.6 kN/m