


Höhe Struktur h_{struc} für Systeme mit Standardbodenaufbau

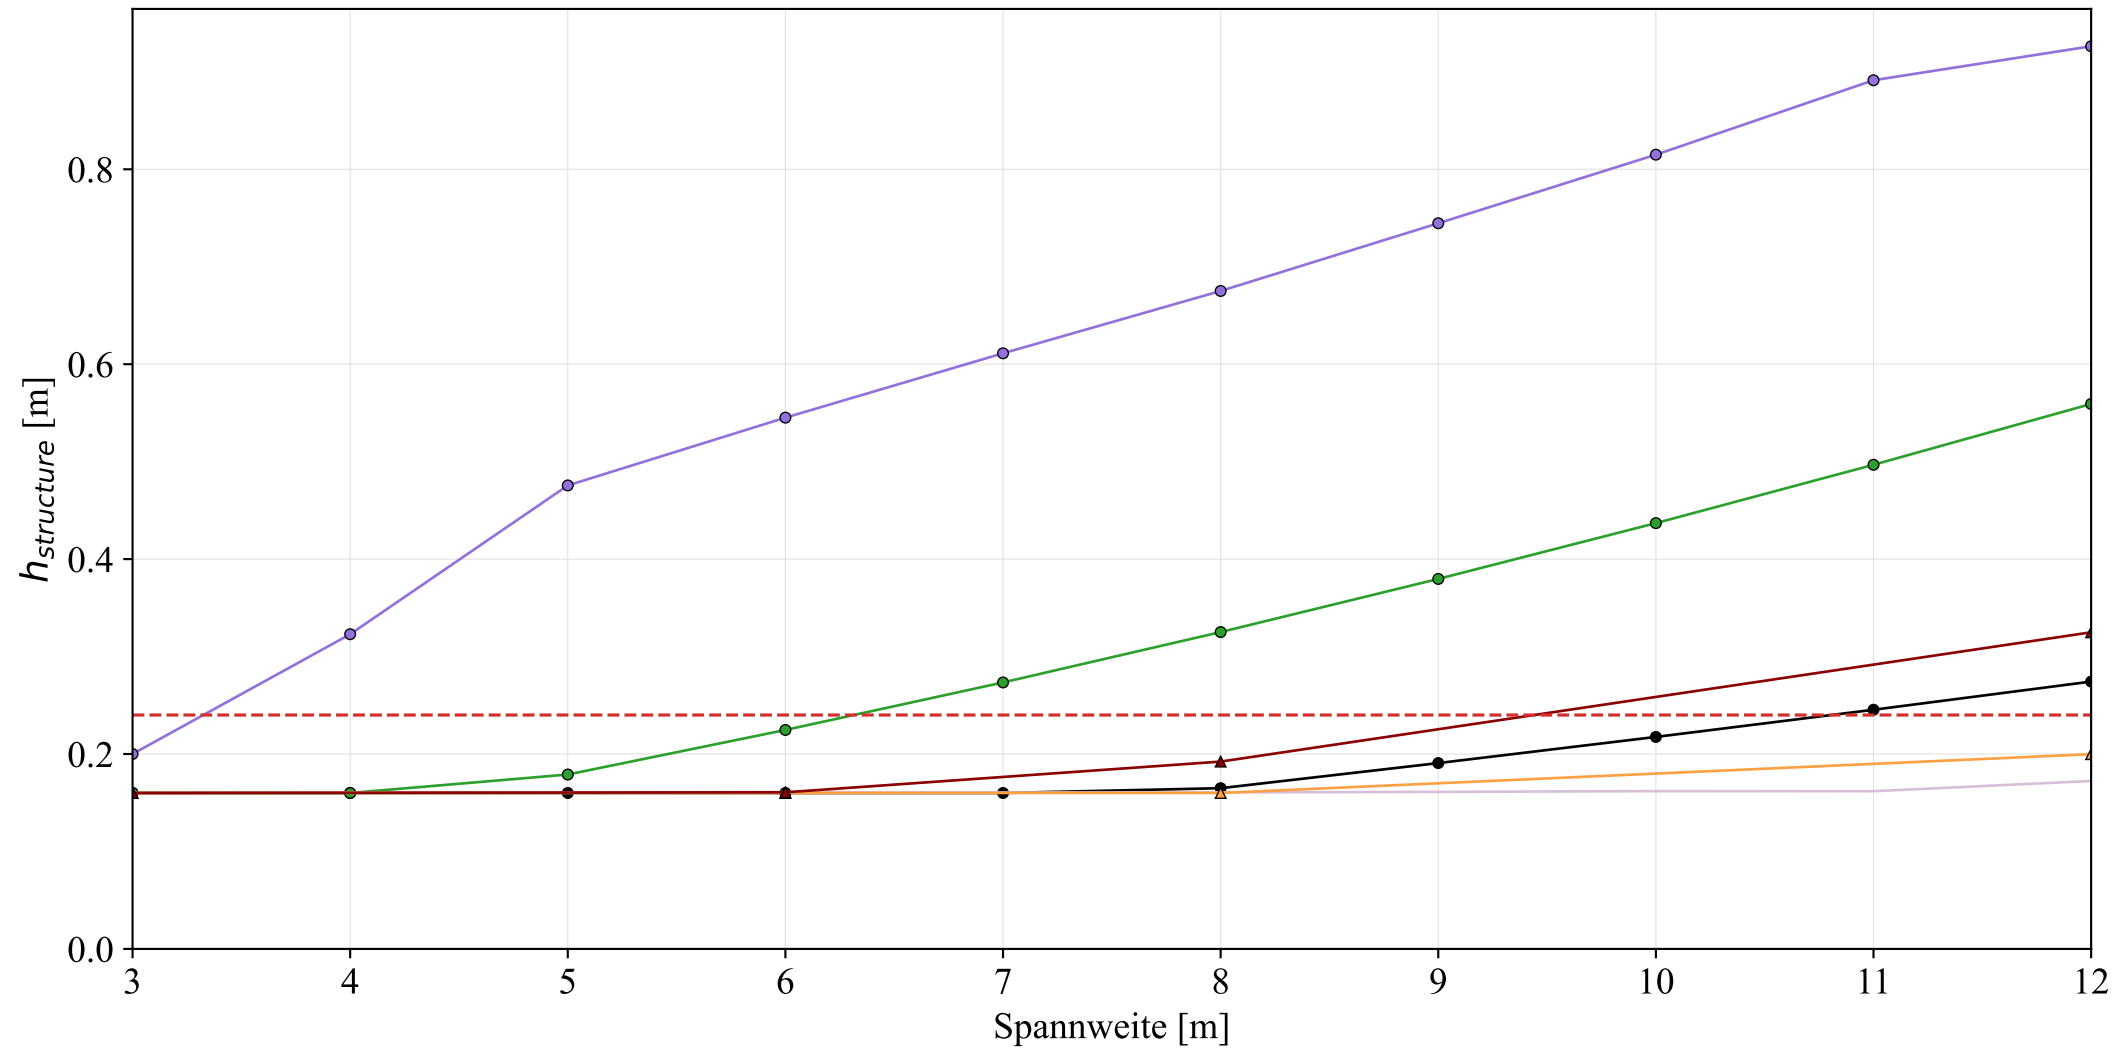

--- Mindeststärke Schallschutz für erhöhte Anforderungen (24 cm)

—▲— Platte liniengelagert, eingespannt (Standardaufbau)

—▲— Platte liniengelagert, frei aufgelegt (Standardaufbau)

—○— Plattenbalken, frei aufgelegt (Standardaufbau)

— Plattenbalken, frei aufgelegt (Standardaufbau), Flanschhöhe