


Einfeldträger vs. Durchlaufträger (3-12m)

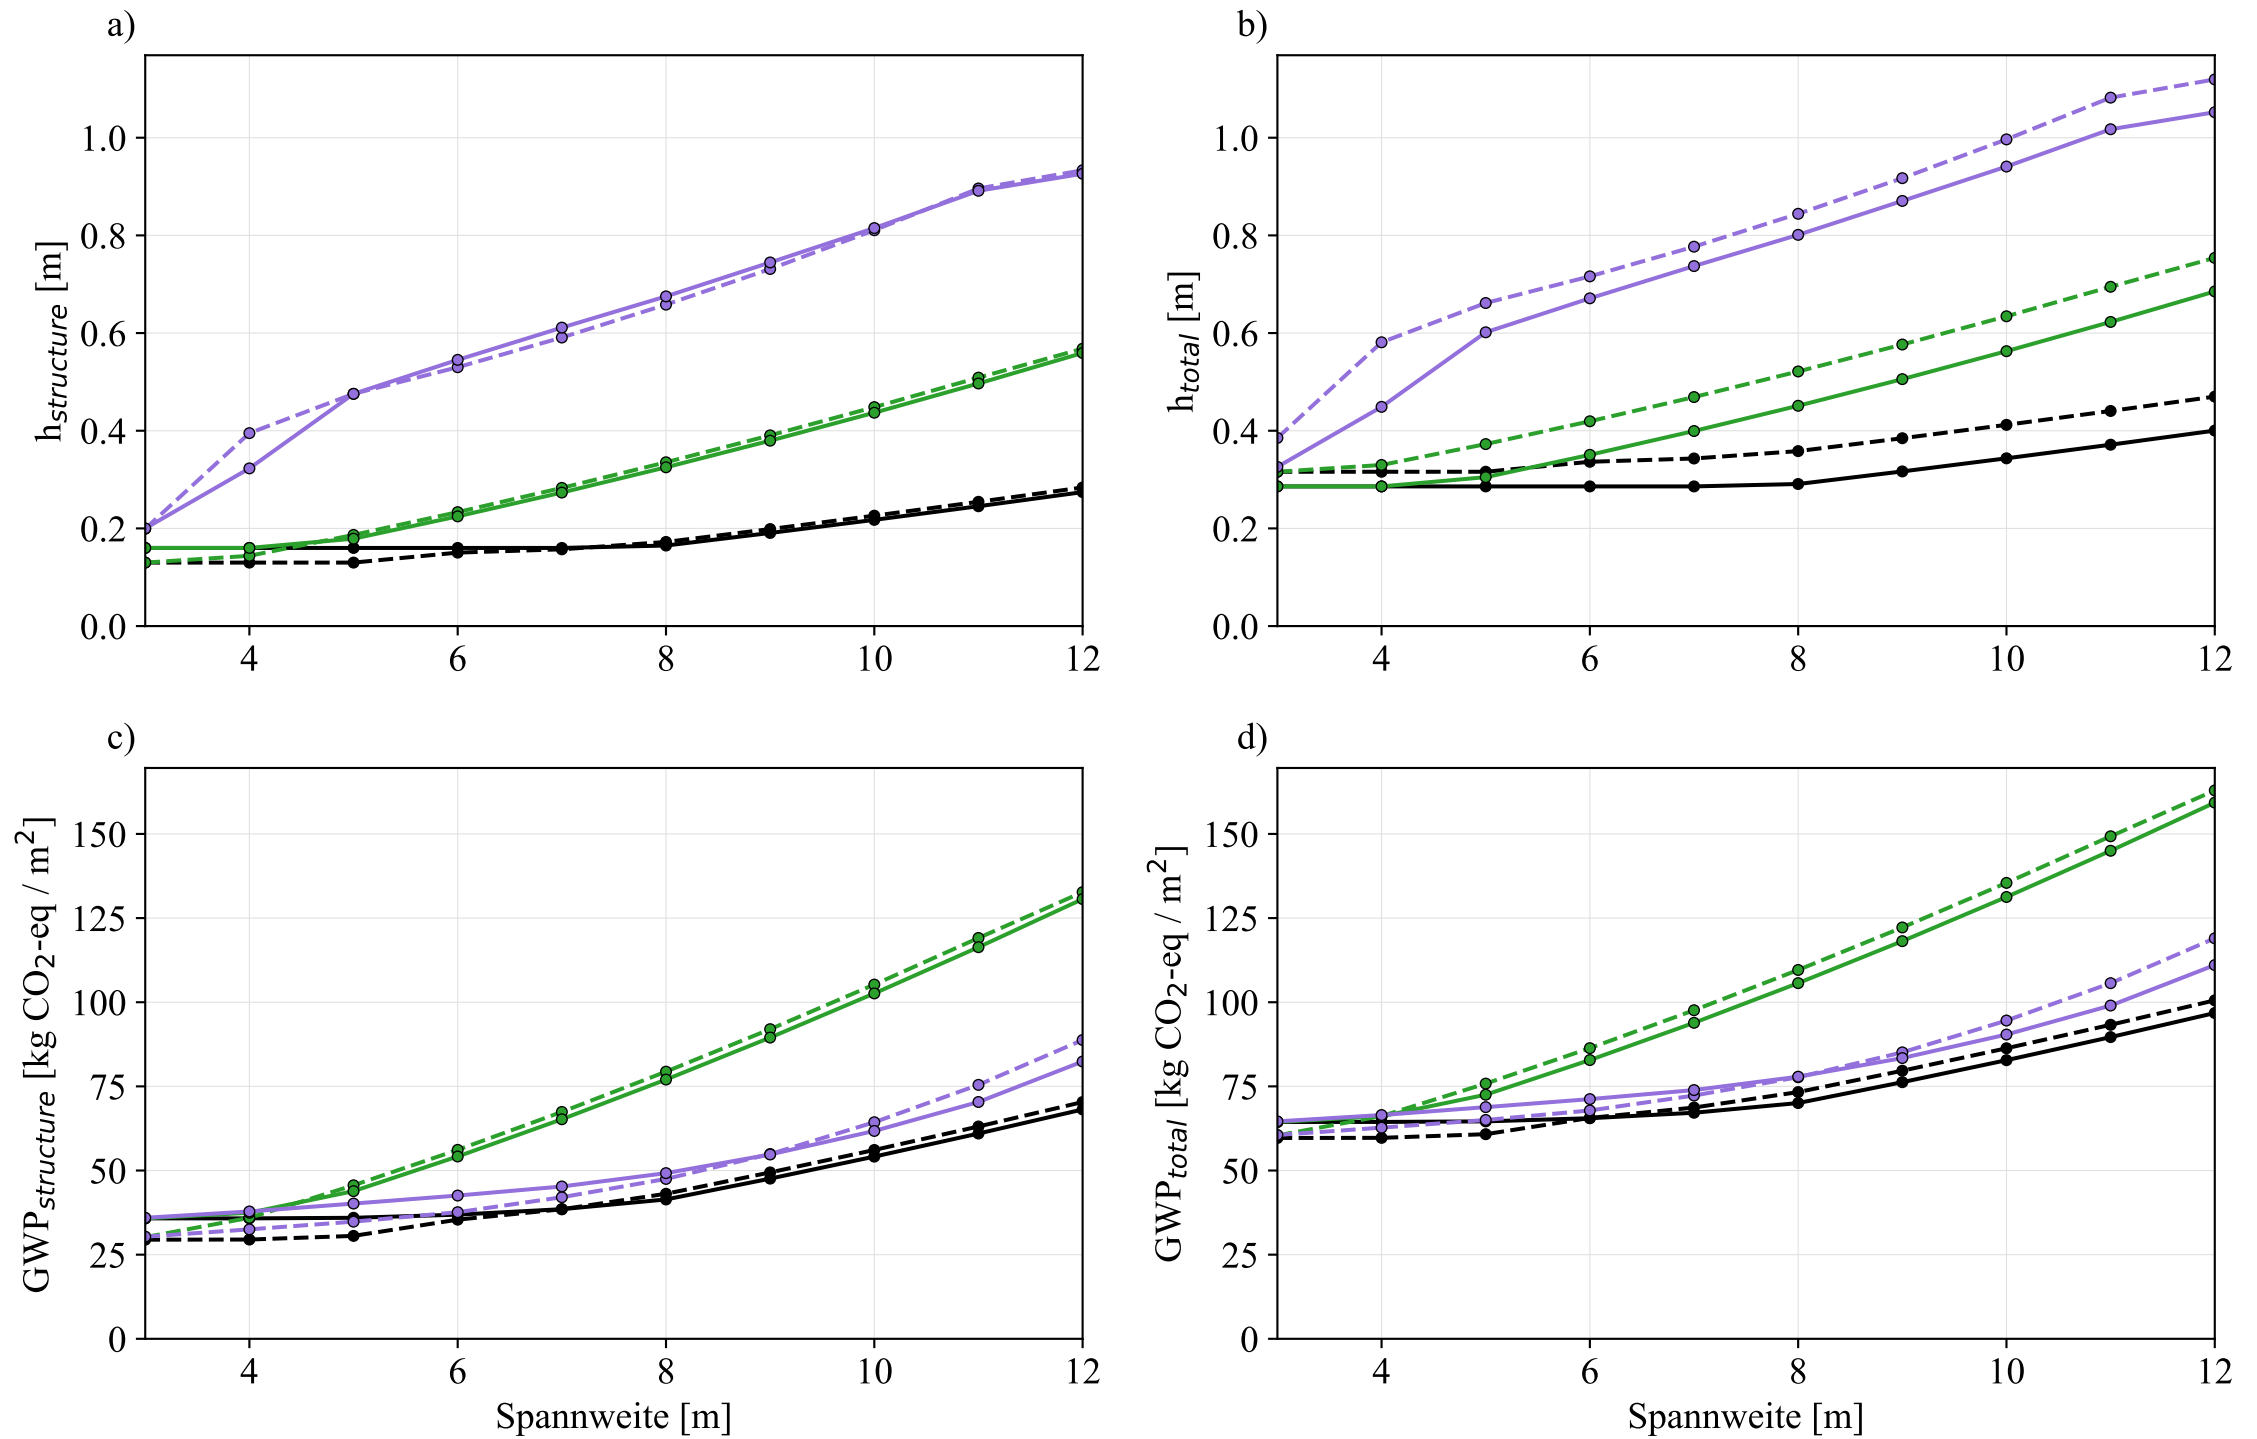

- Vollplatte, einachsig tragend, durchlaufend (Standardaufbau)
- -●- - - Vollplatte, einachsig tragend, durchlaufend (Standardaufbau + Schüttung)
- Vollplatte, einachsig tragend, einfach gelagert (Standardaufbau)
- -●- - - Vollplatte, einachsig tragend, einfach gelagert (Standardaufbau + Schüttung)
- Rippenplatte, einachsig tragend, einfach gelagert (Standardaufbau)
- -●- - - Rippenplatte, einachsig tragend, einfach gelagert (Standardaufbau + Schüttung)