


Einfeldträger vs. Durchlaufträger (3-8m)

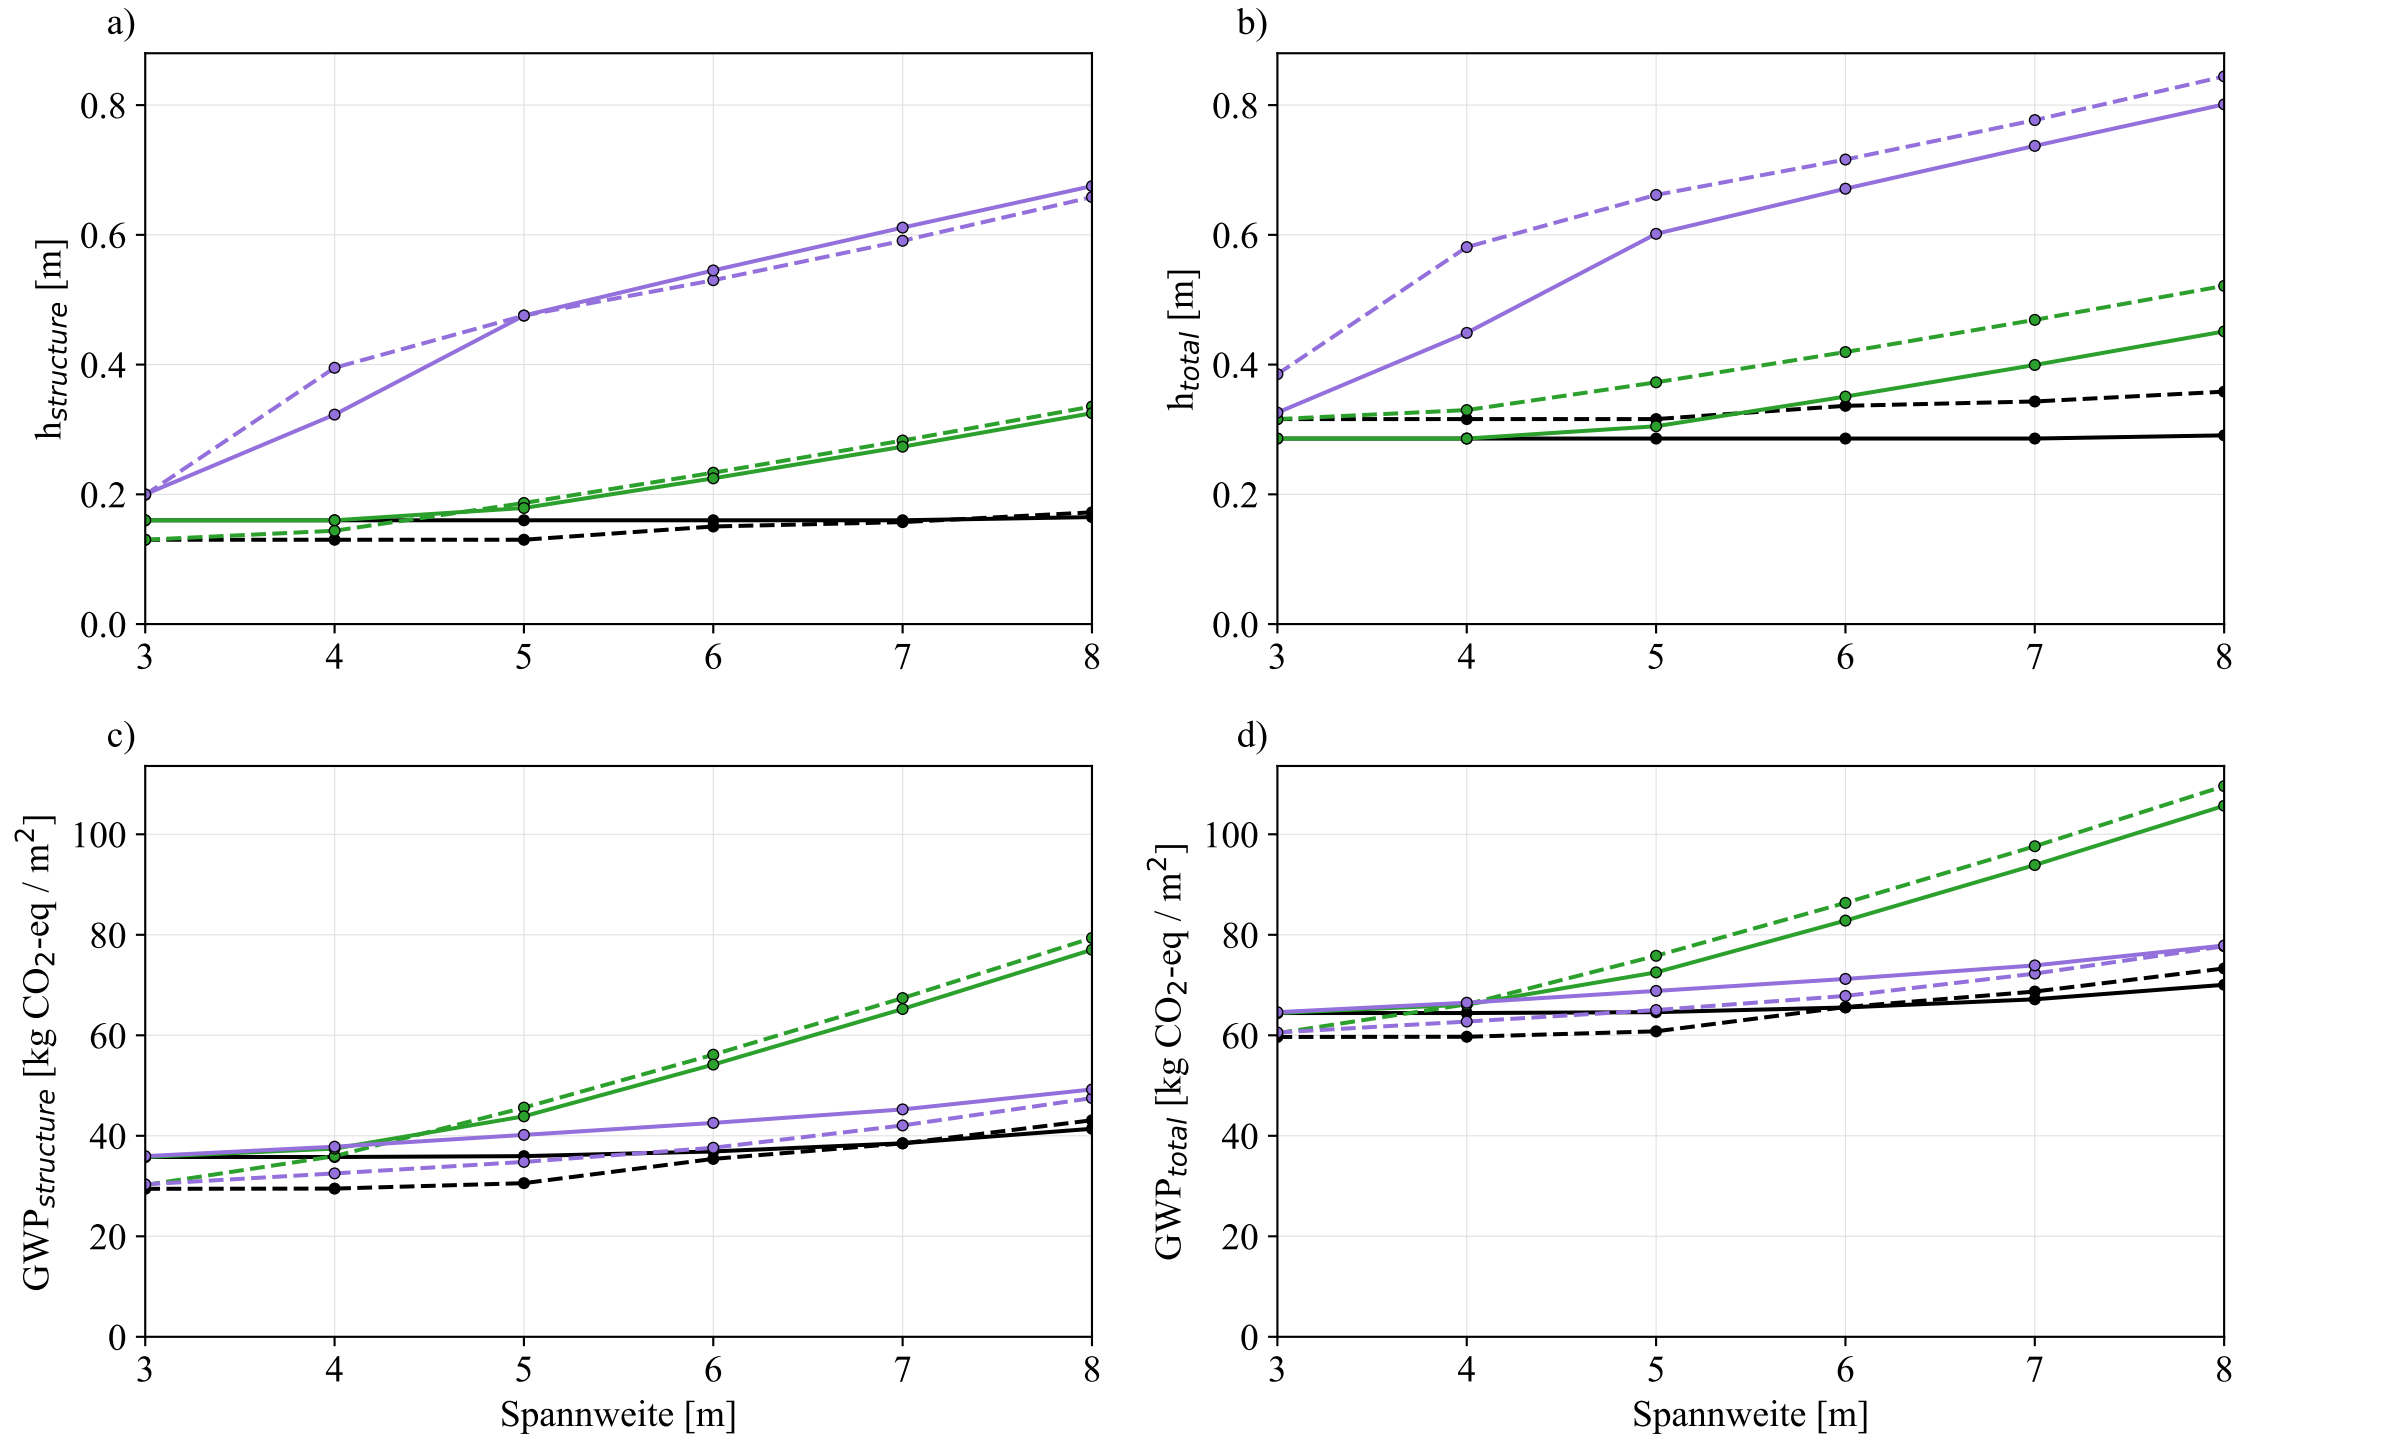

- | | | |
|--|--|--|
| Vollplatte, einachsig tragend, durchlaufend (Standardaufbau) | Vollplatte, einachsig tragend, einfach gelagert (Standardaufbau) | Rippenplatte, einachsig tragend, einfach gelagert (Standardaufbau) |
| Vollplatte, einachsig tragend, durchlaufend (Standardaufbau + Schüttung) | Vollplatte, einachsig tragend, einfach gelagert (Standardaufbau + Schüttung) | Rippenplatte, einachsig tragend, einfach gelagert (Standardaufbau + Schüttung) |