


Höhe Struktur h_{struc} für Systeme mit Standardbodenaufbau

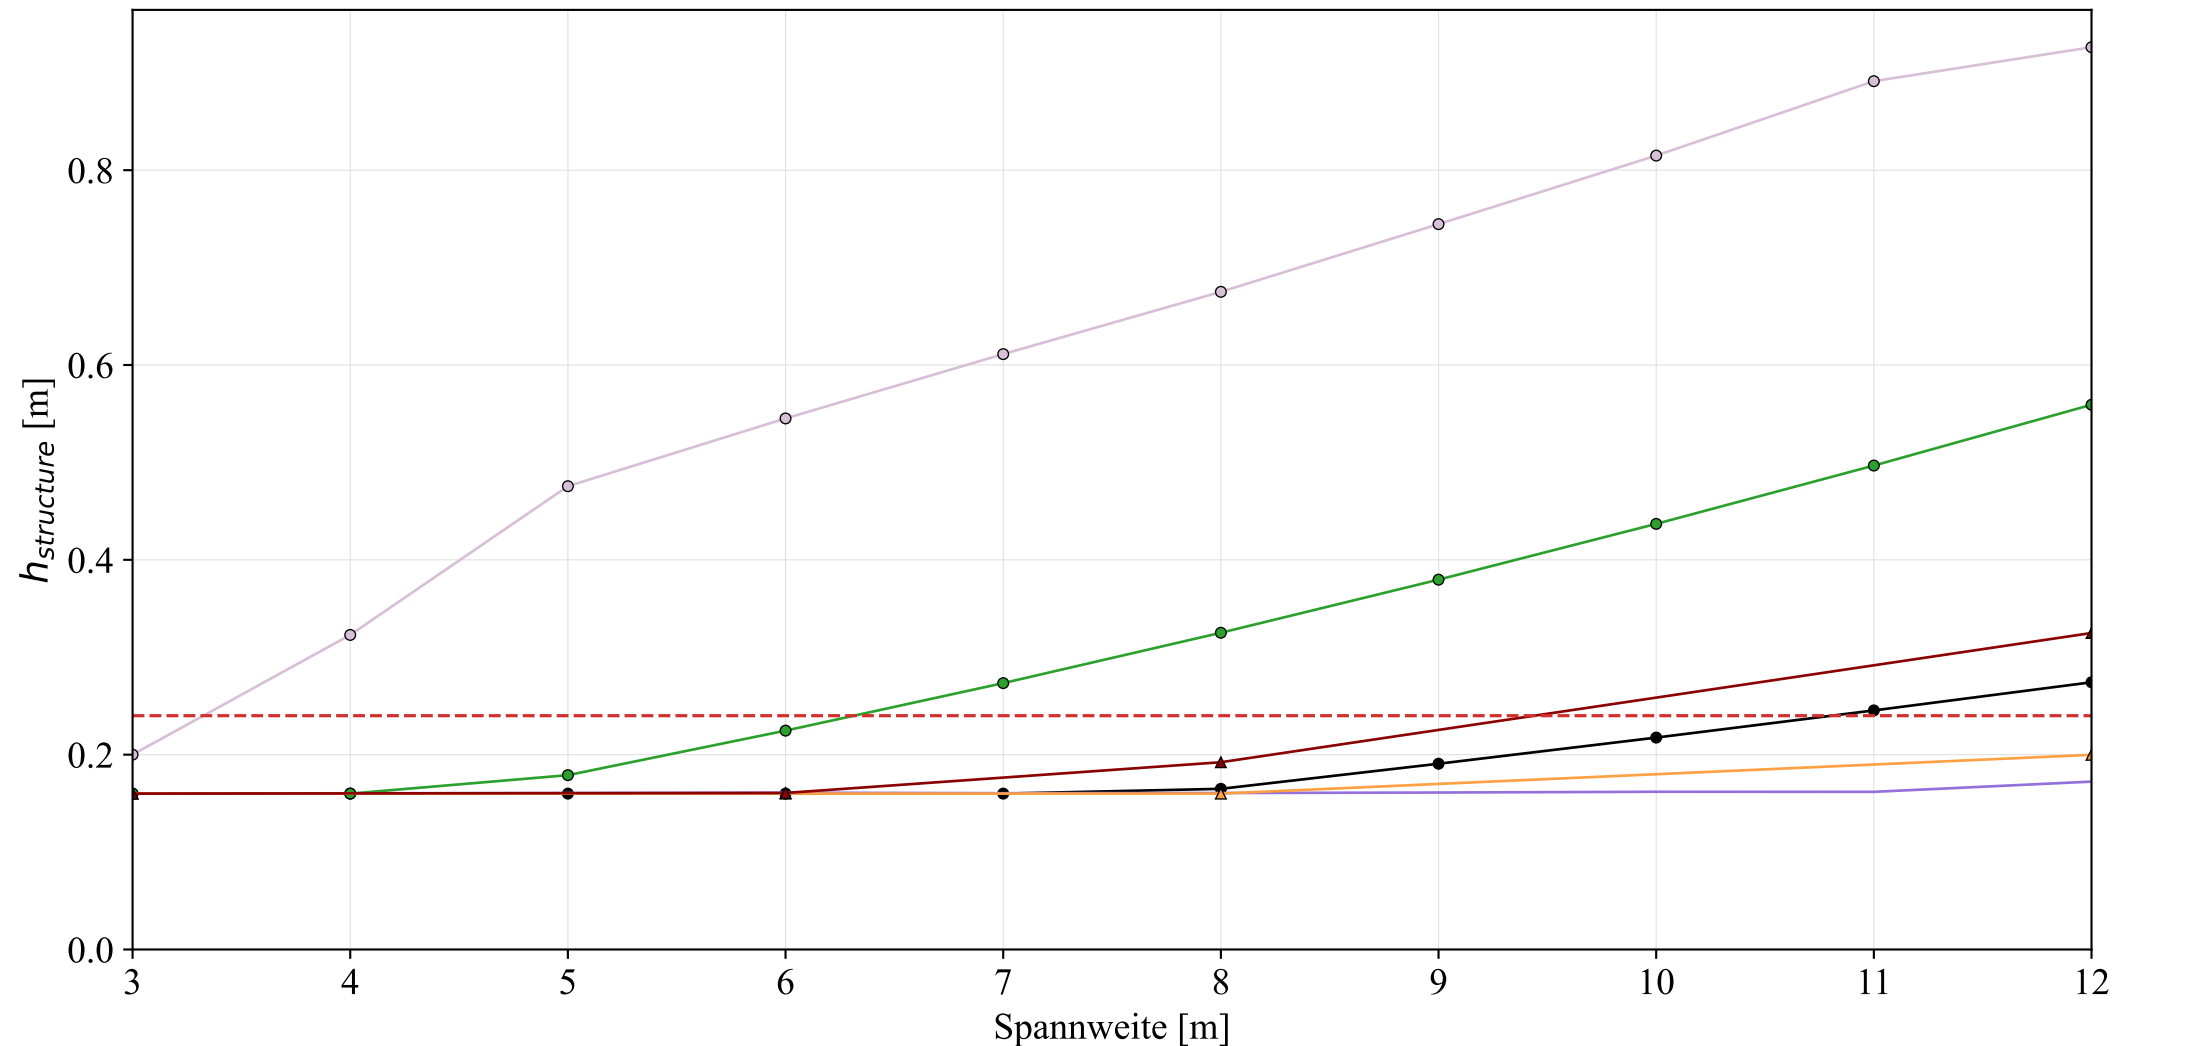

- Vollplatte, einachsig tragend, einfach gelagert (Standardaufbau)
- Vollplatte, einachsig tragend, durchlaufend (Standardaufbau)
- - - Mindeststärke für erhöhte Schallschutzanforderungen (24 cm)
- ▲— Vollplatte, zweiachsig tragend, einfach gelagert (Standardaufbau)
- ▲— Vollplatte, zweiachsig tragend, durchlaufend (Standardaufbau)
- Plattenbalken, einachsig tragend, einfach gelagert (Standardaufbau)
- Plattenbalken, einachsig tragend, einfach gelagert (Standardaufbau), Flanschhöhe