


Einfeldträger vs. Durchlaufträger (3-12m)

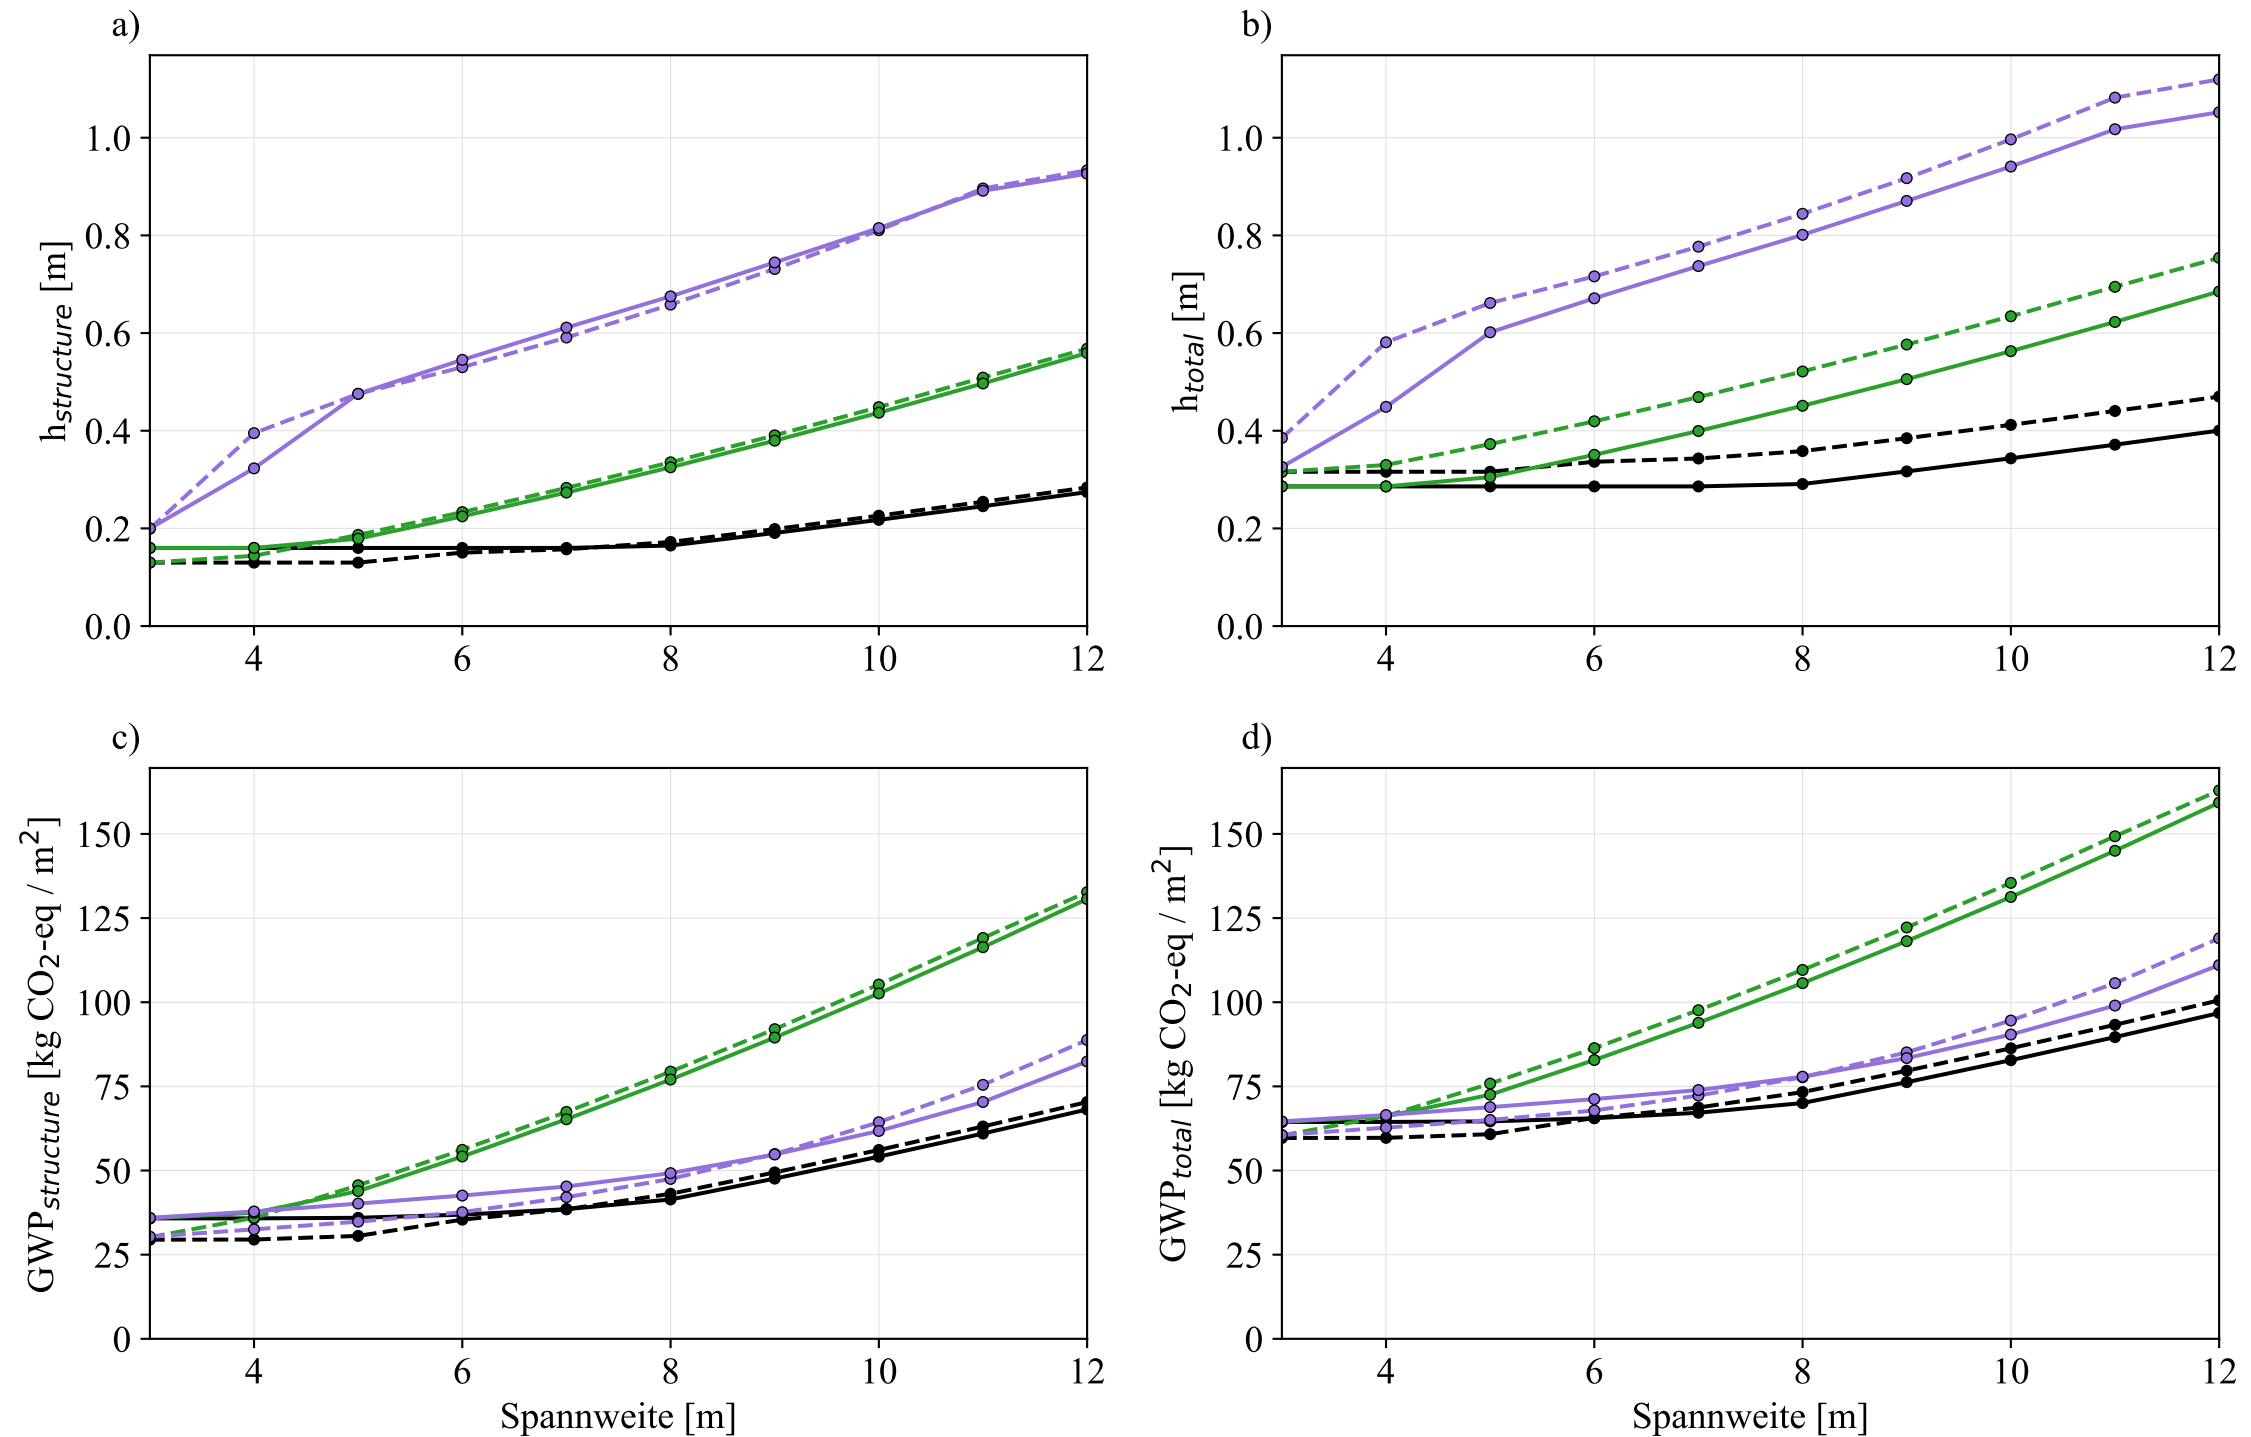

- | | | | | | |
|--|--|--|---|--|---|
| | Plattenstreifen, eingespannt
(Standardaufbau) | | Plattenstreifen, frei aufgelegt
(Standardaufbau) | | Plattenbalken, frei aufgelegt
(Standardaufbau) |
| | Plattenstreifen, eingespannt
(Standardaufbau + Schüttung) | | Plattenstreifen, frei aufgelegt
(Standardaufbau + Schüttung) | | Plattenbalken, frei aufgelegt
(Standardaufbau + Schüttung) |