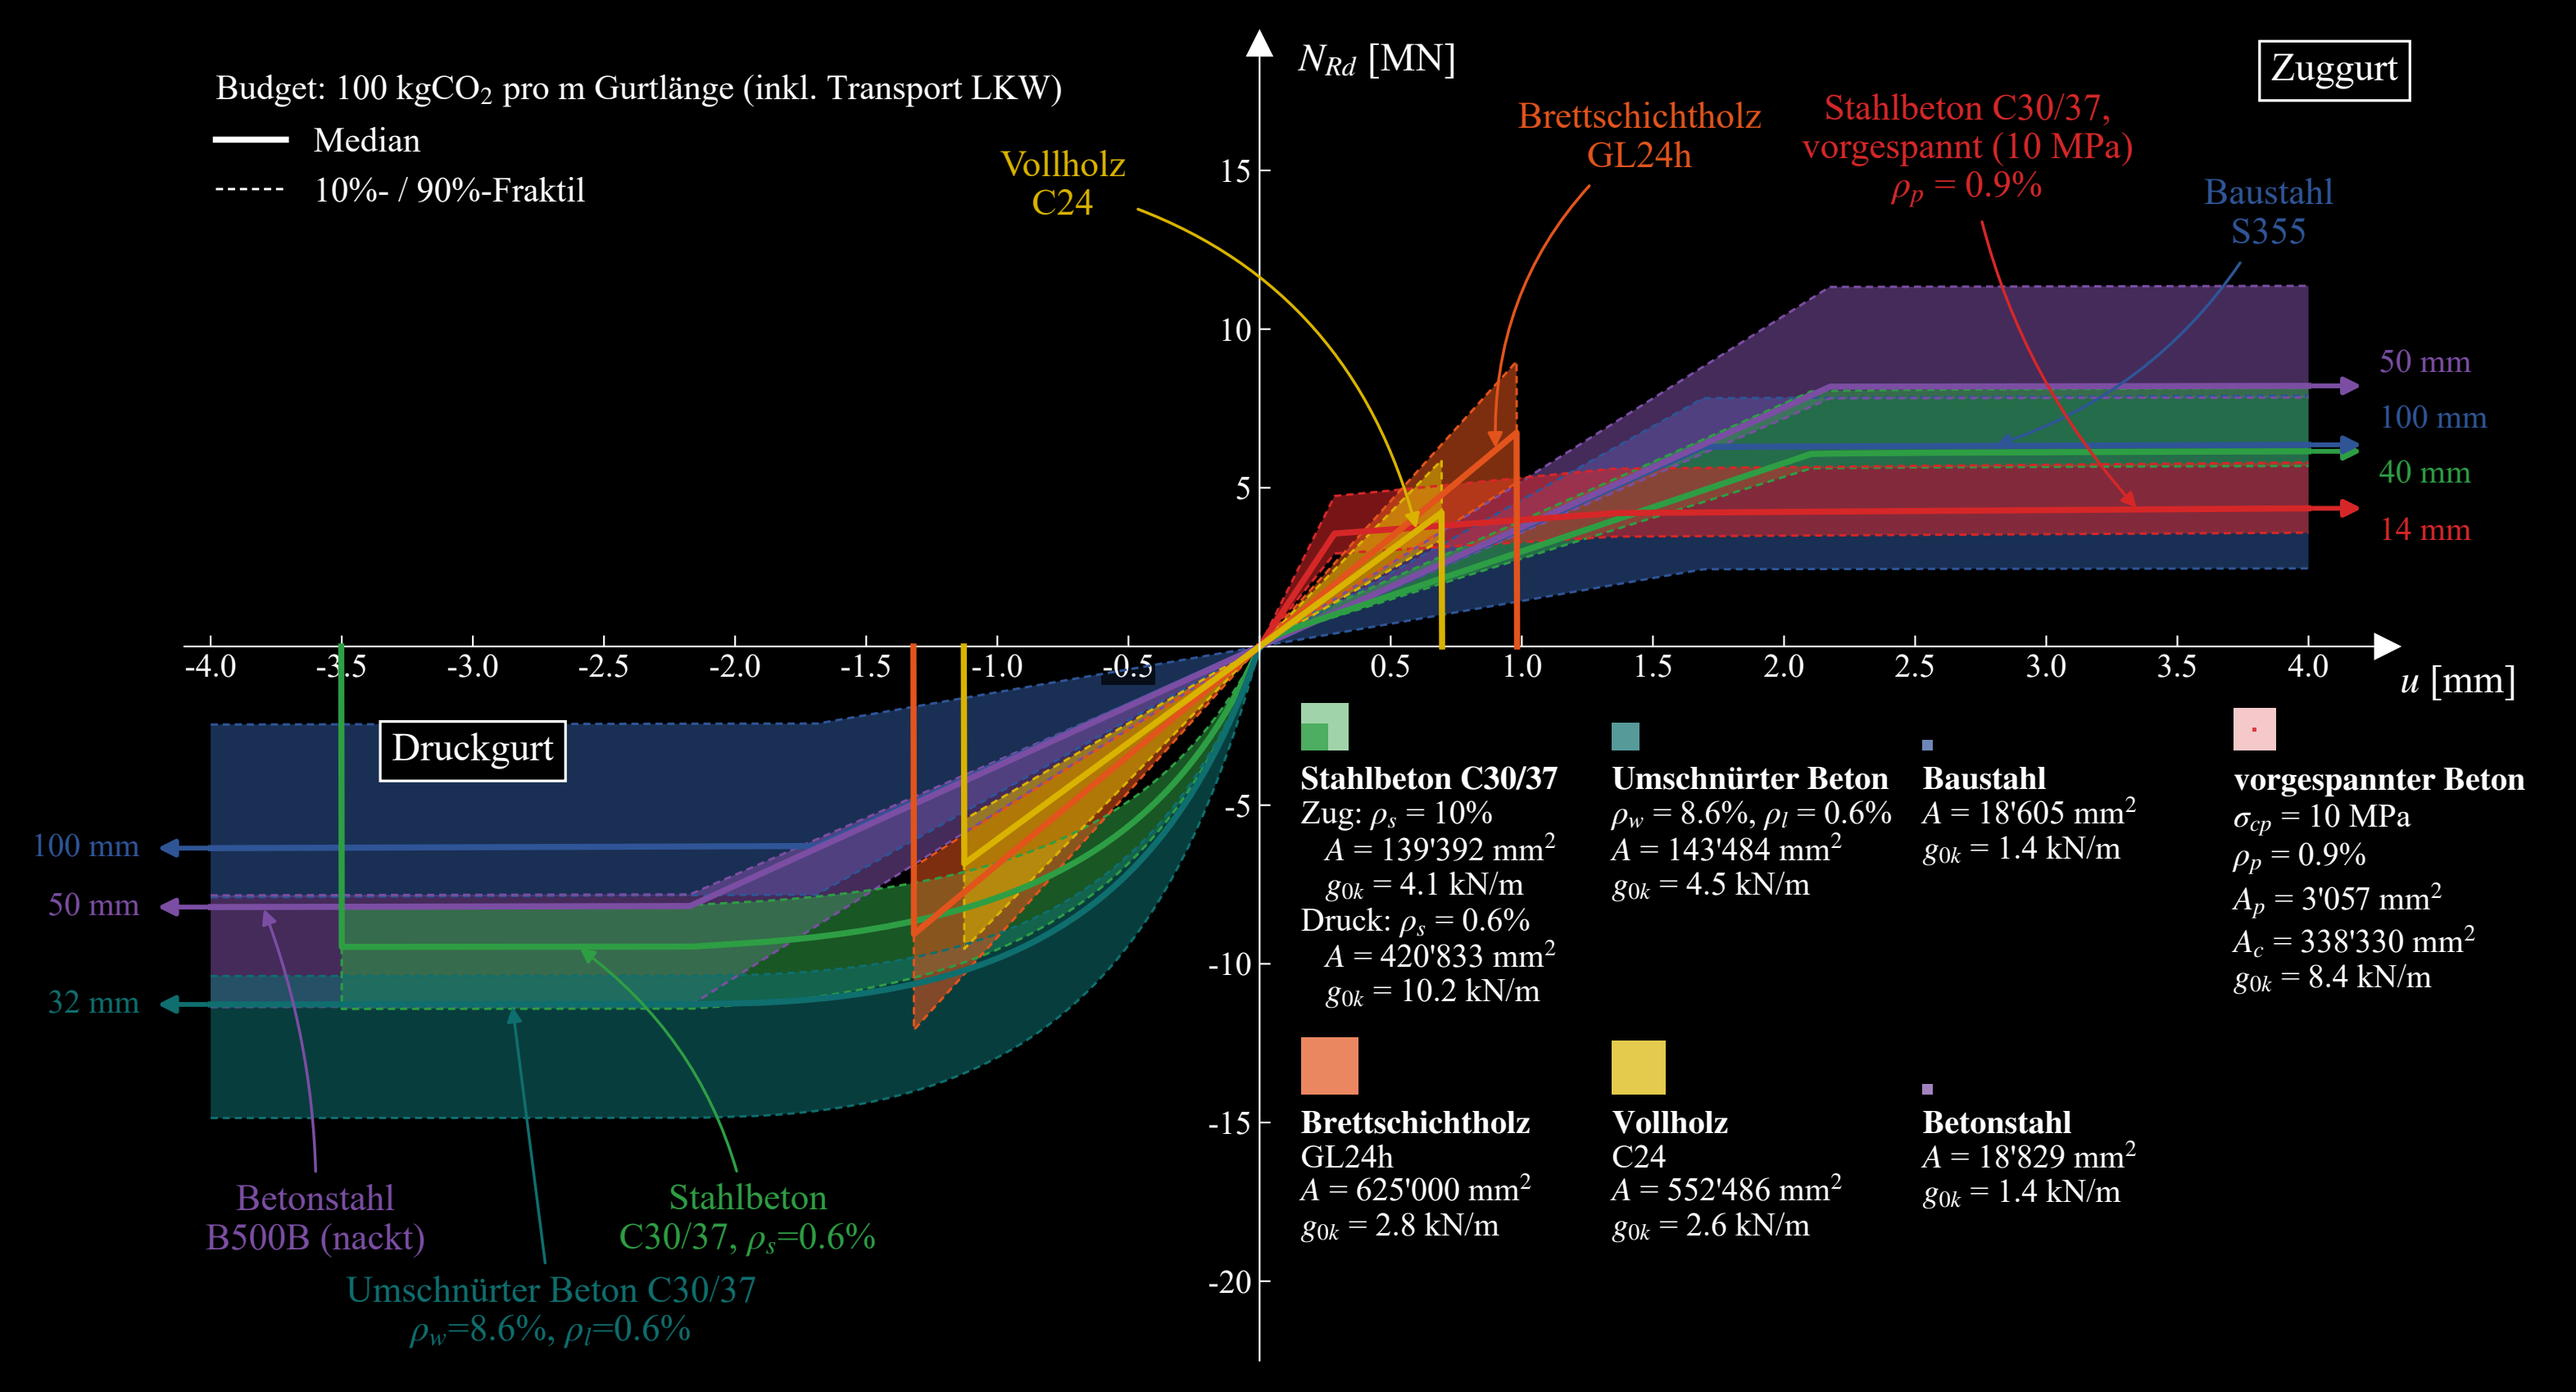

Budget: 100 kgCO2 pro m Gurtlänge (inkl. Transport LKW)
Median
10%- / 90%-Fraktil
NRd [MN]
Zuggurt
Vollholz C24
Brettschichtholz GL24h
Stahlbeton C30/37, vorgespannt (10 MPa) ρp = 0.9%
Baustahl S355
50 mm
100 mm
40 mm
14 mm
15
10
5
-5
-10
-15
-20
-4.0
-3.5
-3.0
-2.5
-2.0
-1.5
-1.0
-0.5
0.5
1.0
1.5
2.0
2.5
3.0
3.5
4.0
u [mm]
Druckgurt
100 mm
50 mm
32 mm
Betonstahl B500B (nackt)
Umschnürter Beton C30/37 ρw=8.6%, ρl=0.6%
Stahlbeton C30/37, ρs=0.6%
Stahlbeton C30/37
Zug: ρs = 10%
A = 139'392 mm2
g0k = 4.1 kN/m
Druck: ρs = 0.6%
A = 420'833 mm2
g0k = 10.2 kN/m
Umschnürter Beton
ρw = 8.6%, ρl = 0.6%
A = 143'484 mm2
g0k = 4.5 kN/m
Baustahl
A = 18'605 mm2
g0k = 1.4 kN/m
vorgespannter Beton
σcp = 10 MPa
ρp = 0.9%
Ap = 3'057 mm2
Ac = 338'330 mm2
g0k = 8.4 kN/m
Brettschichtholz
GL24h
A = 625'000 mm2
g0k = 2.8 kN/m
Vollholz
C24
A = 552'486 mm2
g0k = 2.6 kN/m
Betonstahl
A = 18'829 mm2
g0k = 1.4 kN/m