Quellenbeleg der abgelesenen Spannweiten und Deckenstärken


Bestandesanalyse Wohnbauten, Projekt «Nachhaltigkeit im Tragwerksentwurf», kfm research group, IBK, ETH Zürich

Erstellt am 11.11.2026 aus den Originalplänen in «01_Daten und Pläne».

Jede Seite zeigt den Planausschnitt, aus dem der Wert gelesen wurde. Rot markiert ist die Stelle der Masskette.


Die zugehörigen Zahlenwerte stehen im Blatt «Objekte» des Excels Bestandesanalyse_Wohnbauten.

1. Dietlikon

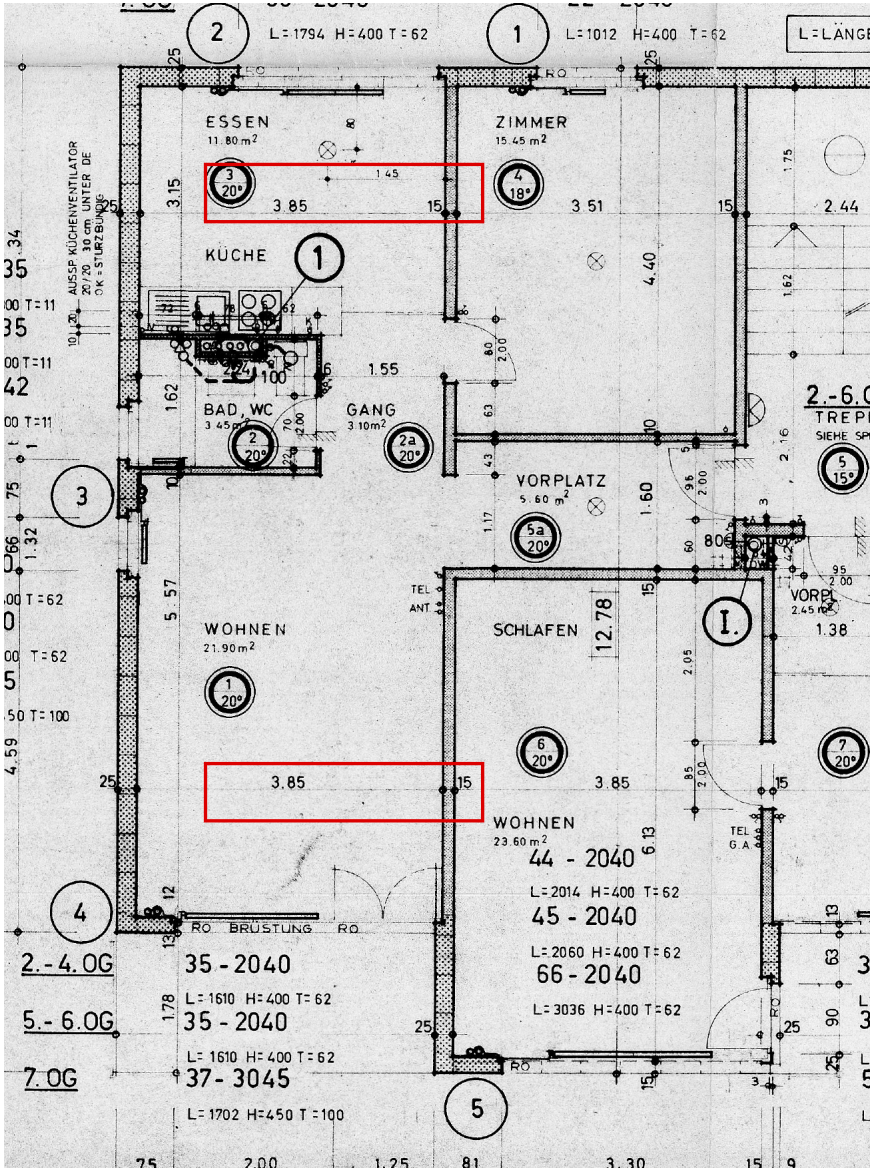


Datei:	ABZ/Dietlikon/Pläne 1_50/Haus A+B 2.-7. Obergeschoss.pdf
Seite, Massstab, Datum:	Seite 1, 1:50, 1968
Abgelesen:	Lichte Raumbreite 3.85 m zwischen Durisol-Aussenwand 25 cm und Innenwand 15 cm, Raumtiefe 5.57 m. Achsmass der kurzen Richtung 4.05 m.
Verwendet als:	massgebende Spannweite 4.05 m

2. Glattpark

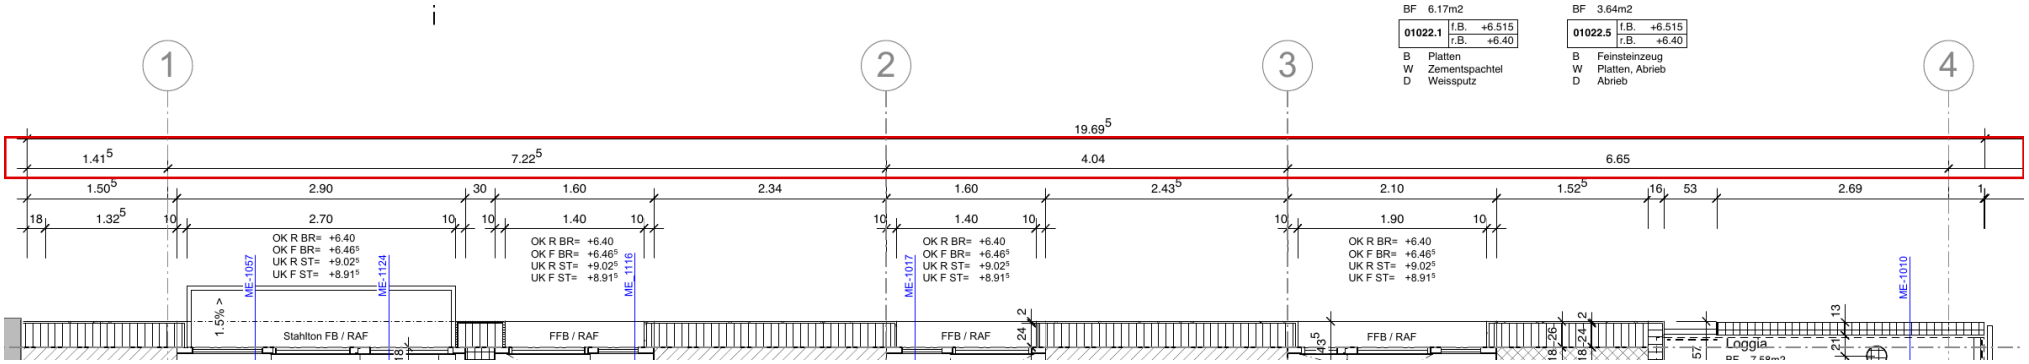

Datei:	ABZ/Glattpark/6.23 Architekt/Rev Werkpläne 1 zu 50 Nordareal/Grundrisse/AN/53-AR-AN-GA-GR-O2-WER-0105-_.pdf
Seite, Massstab, Datum:	Seite 1, 1:50, 2017
Abgelesen:	Masskette der Achsen 1...4: 7.22 m, 4.04 m, 6.65 m.
Verwendet als:	längere Rasterachse des massgebenden Feldes 7.22 m

3. Glattpark

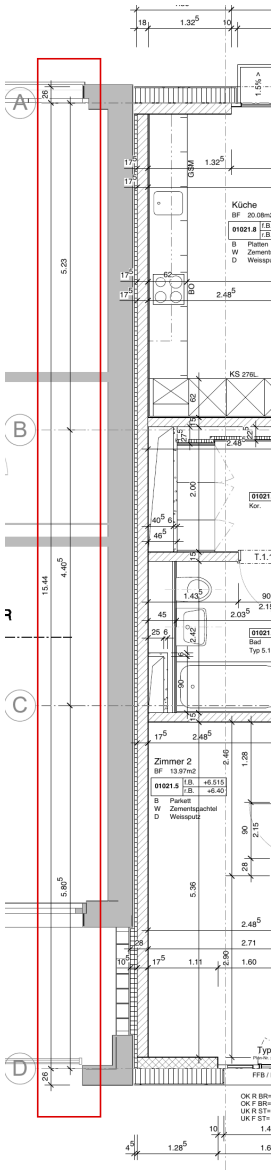


Datei: ABZ/Glattpark/6.23 Architekt/Rev Werkpläne 1 zu 50 Nordareal/Grundrisse/AN/53-AR-AN-GA-GR-O2-WER-0105-_.pdf

Seite, Massstab, Datum: Seite 1, 1:50, 2017

Abgelesen: Masskette der Achsen A...D: 5.23 m, 4.41 m, total 15.44 m, unteres Feld 5.81 m.


Verwendet als: kürzere Spannweite des massgebenden Feldes 5.81 m

4. Regina Kägi Hof, Zeile 2

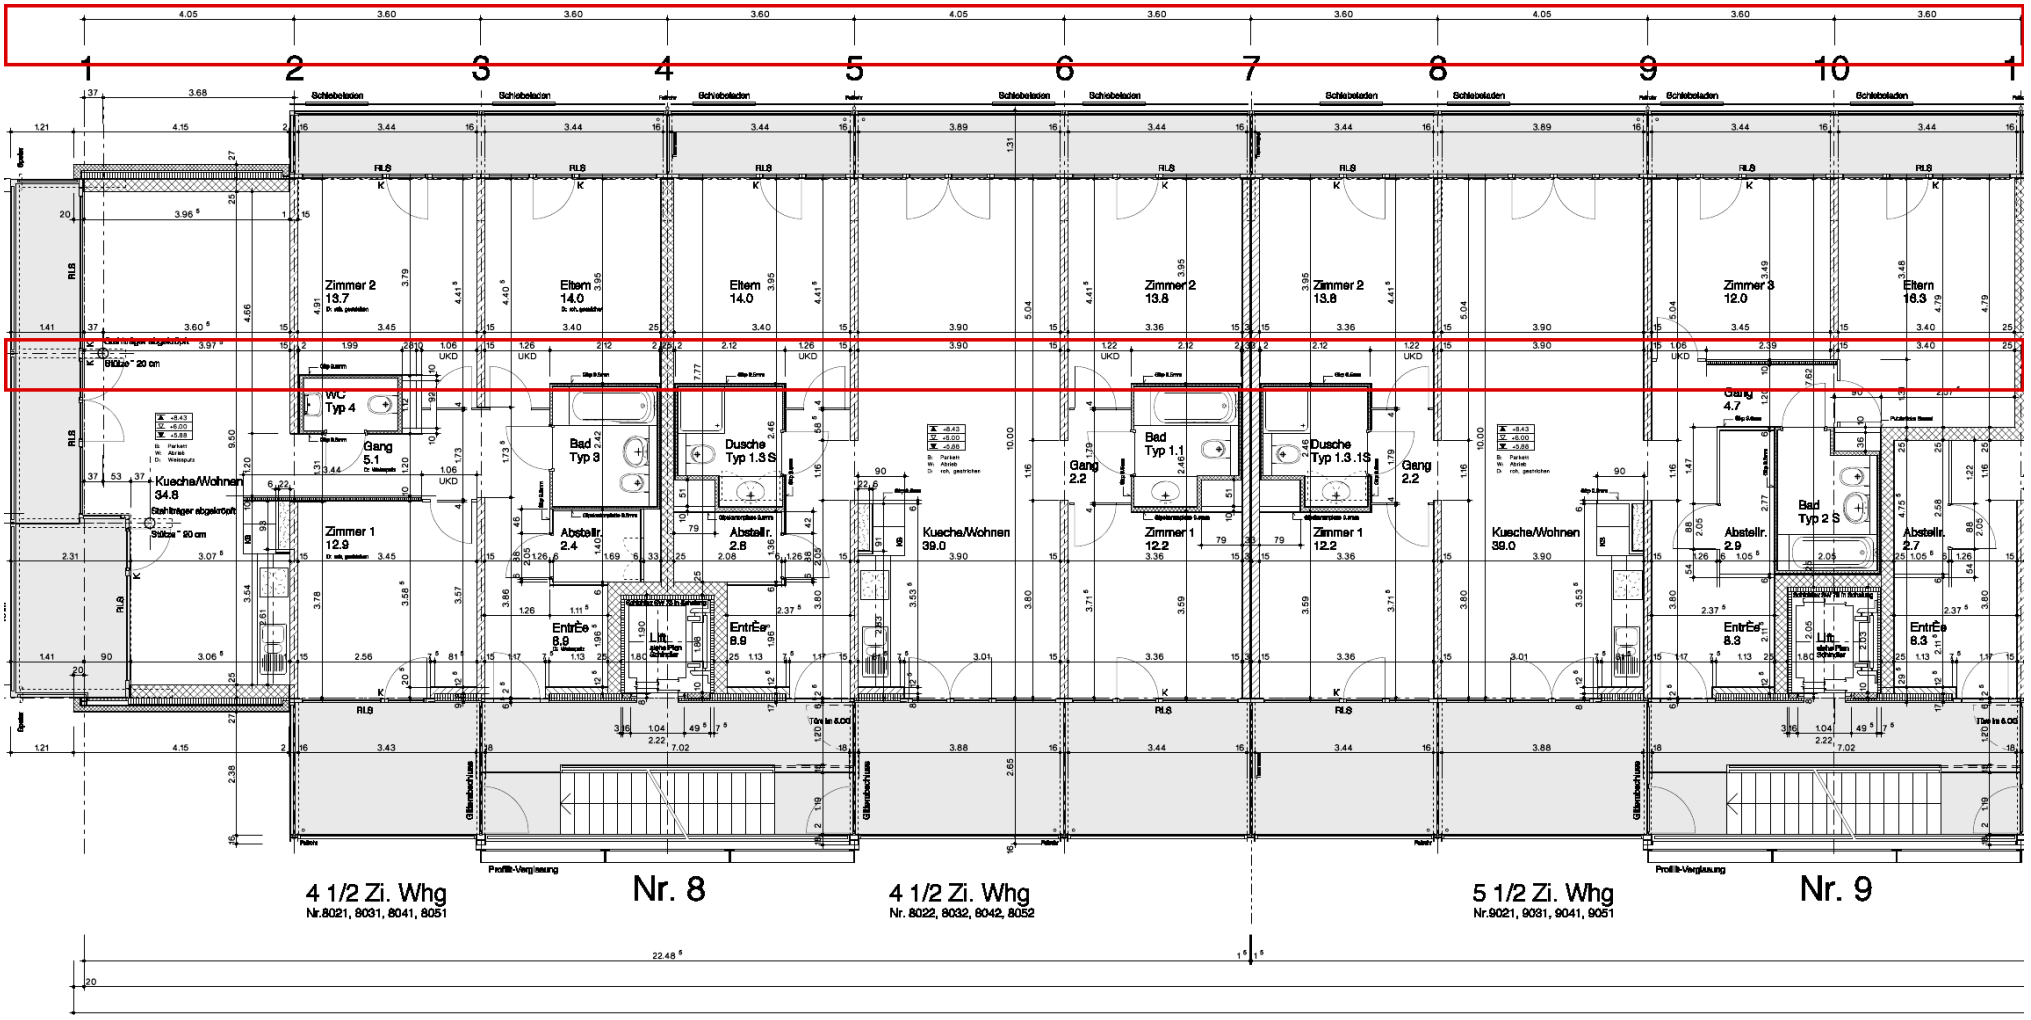


Datei:	ABZ/Regina Kägi Hof/6000_2001_Rev. Plan_2.-4. OG Solitär_2.-5. OG Zeilen.pdf
Seite, Massstab, Datum:	Seite 1, 1:100, 2001
Abgelesen:	Achsraster quer 4.05 / 3.60 / 3.60 / 3.60 / 4.05 m, Gebäudetiefe 10.00 m, durch eine Längswand in zwei Felder von rund 5.04 m geteilt.
Verwendet als:	massgebende Spannweite 4.05 m

5. Herrlig

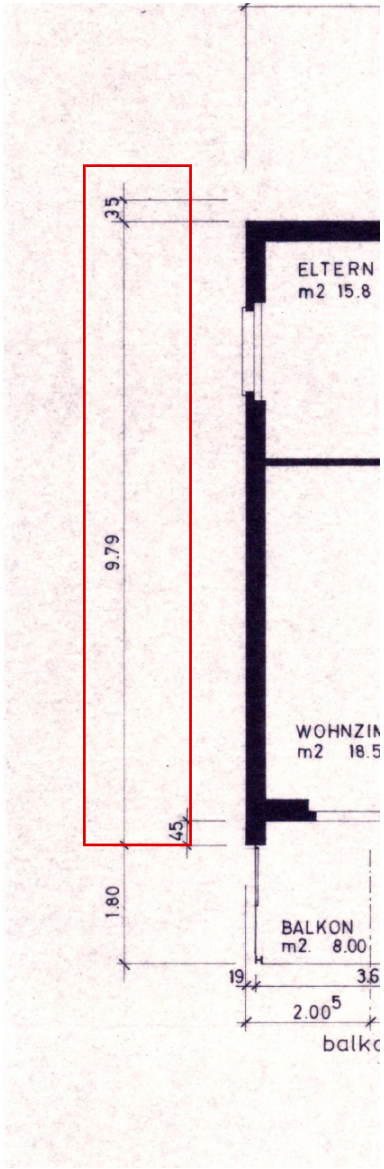


Datei:	ABZ/Herrlig/3500_Plan_GR_SCHN_Block_1-3.pdf
Seite, Massstab, Datum:	Seite 1, 1:100, 1995 (Revisionsplan Bestand 1948)
Abgelesen:	Gebäudetiefe 9.79 m, Balkon 1.80 m. Die Längswand teilt die Tiefe in Bänder von 3.61 m und 5.49 m.
Verwendet als:	massgebende Spannweite 3.61 m (Spannrichtung der Balken angenommen, nicht angeschrieben)

6. Ottostrasse

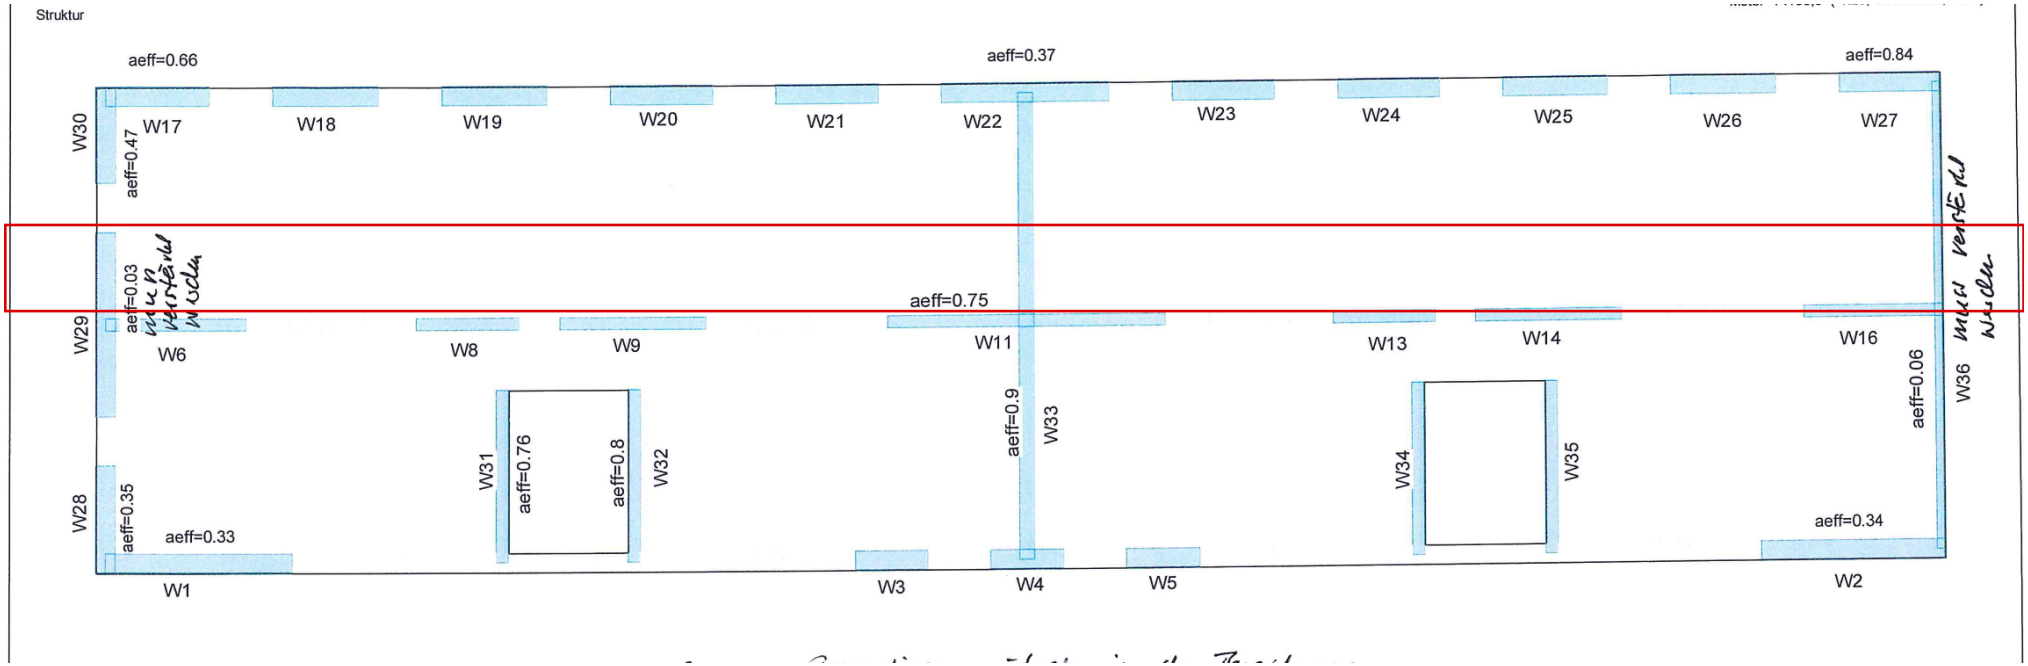

Datei:	ABZ/Ottostrasse/6.25 Bauingenieur/1800_20160429_IS_Beilage Schematischer Grundriss der tragenden Wänden.pdf
Seite, Massstab, Datum:	Seite 1, 1:105.3, 2016 (Erdbebenüberprüfung, Bestand 1927)
Abgelesen:	Schematischer Grundriss der tragenden Wände: Gebäude rund 40.0 x 10.2 m, eine durchlaufende Längswand in der Mitte, Bänder von je rund 5.0 m.
Verwendet als:	massgebende Spannweite 5.0 m

7. Toblerstrasse

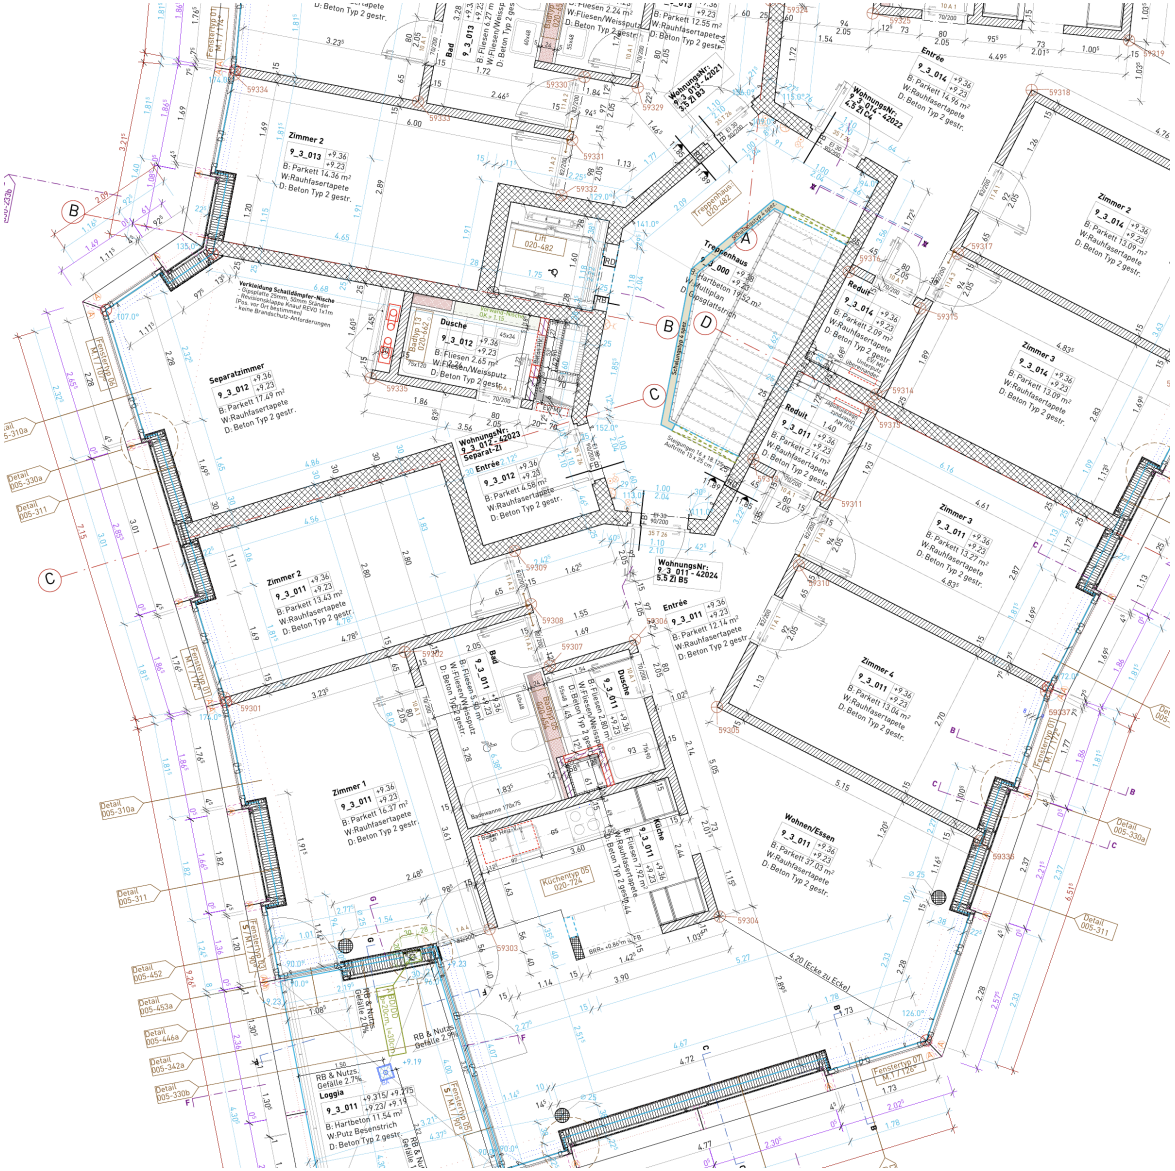


Datei: ABZ/Toblerstrasse/6.23 Architekt/2500_20171106_NB_H9_3_Grundriss.pdf

Seite, Massstab, Datum: Seite 1, 1:50, 2017

Abgelesen: Tragende Betonwände 25 cm, lichte Raummasse 4.56...6.68 m. Der Grundriss ist polygonal, die Deckenfelder sind nicht rechteckig.

Verwendet als: massgebende Spannweite 4.86 m (Interpretation, keine Ingenieurpläne vorhanden)

8. Sihlfeld

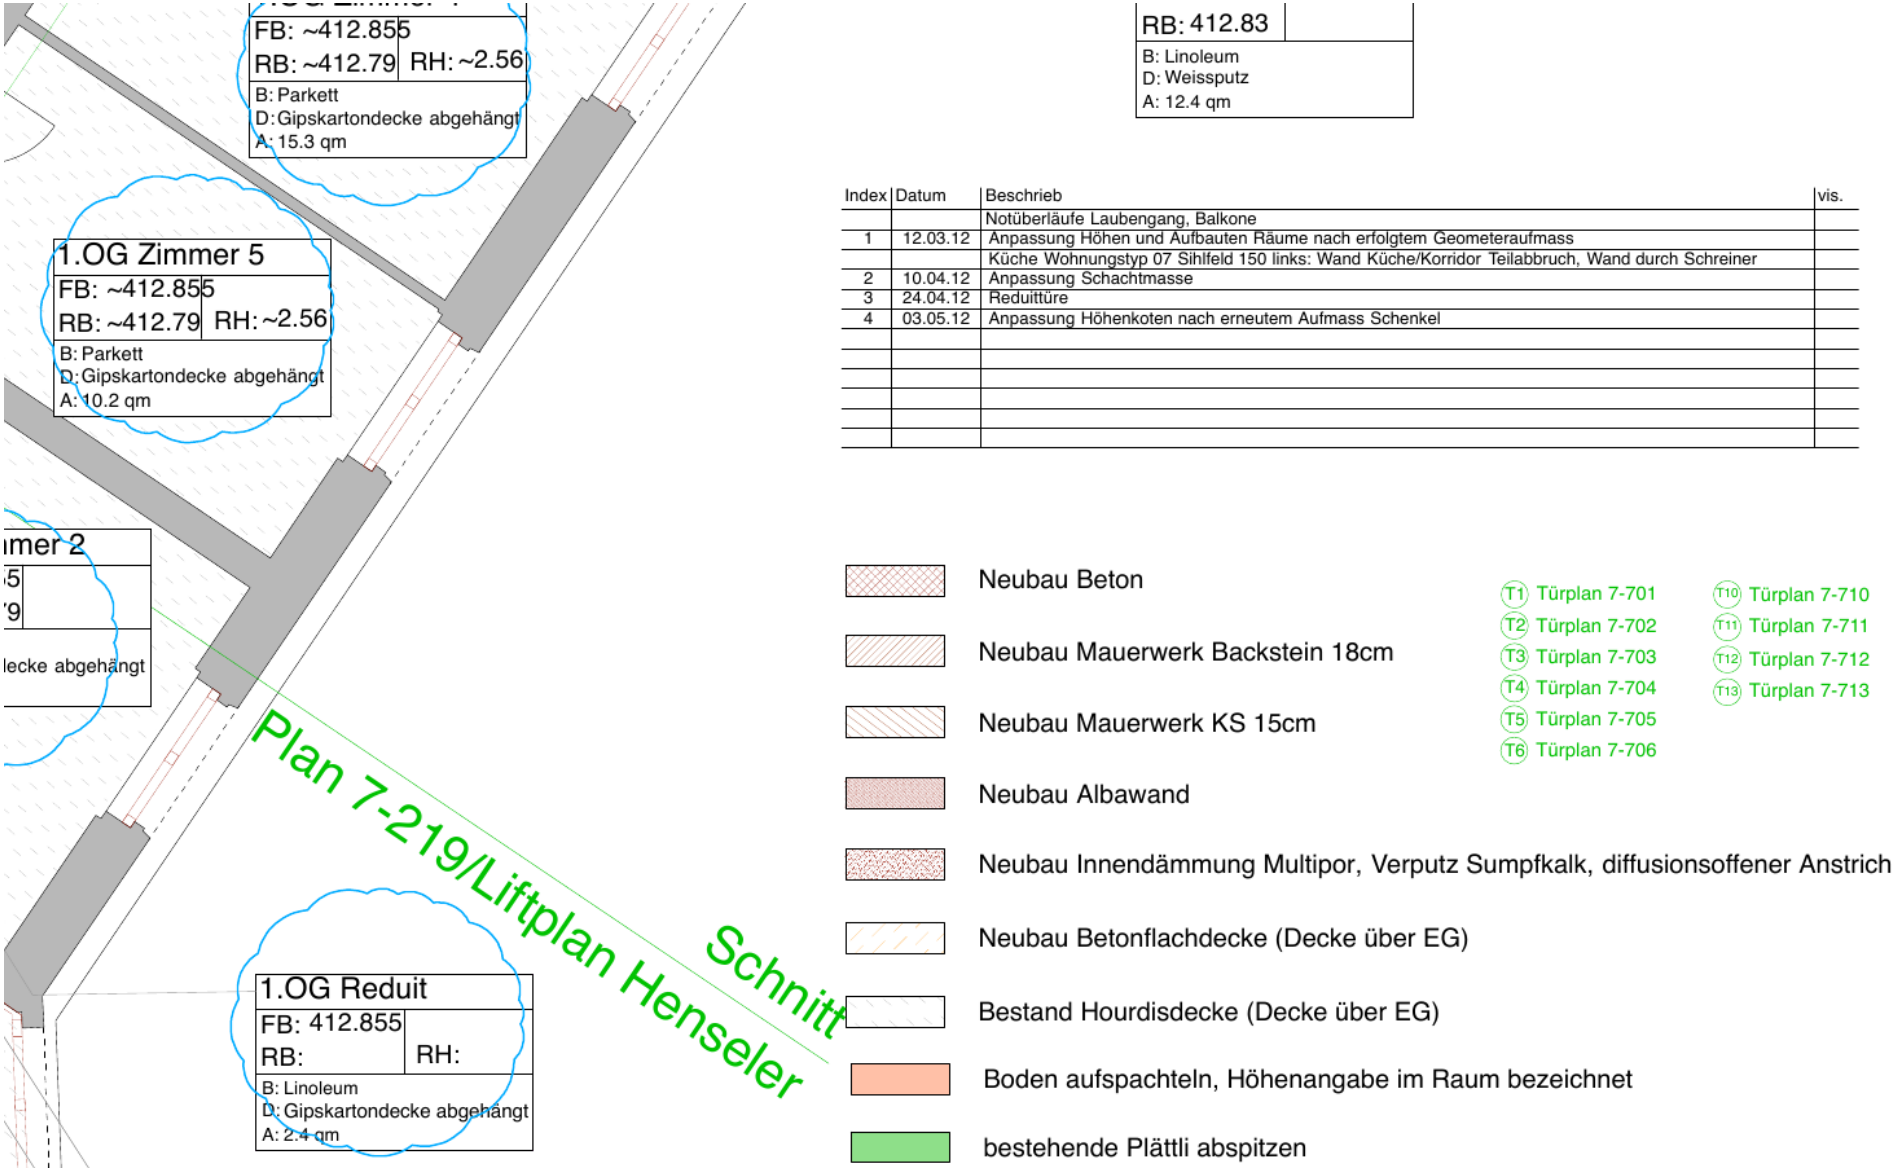

Index	Datum	Beschrieb	vis.
		Notüberläufe Laubengang, Balkone	
1	12.03.12	Anpassung Höhen und Aufbauten Räume nach erfolgtem Geometeraufmass	
		Küche Wohnungstyp 07 Sihlfeld 150 links: Wand Küche/Korridor Teilabbruch, Wand durch Schreiner	
2	10.04.12	Anpassung Schachtmasse	
3	24.04.12	Reduittüre	
4	03.05.12	Anpassung Höhenkoten nach erneutem Aufmass Schenkel	

- Neubau Beton
- Neubau Mauerwerk Backstein 18cm
- Neubau Mauerwerk KS 15cm
- Neubau Albawand
- Neubau Innendämmung Multipor, Verputz Sumpfkalk, diffusionsoffener Anstrich
- Neubau Betonflachdecke (Decke über EG)
- Bestand Hourdisdecke (Decke über EG)
- Boden aufspachteln, Höhenangabe im Raum bezeichnet
- bestehende Plättli abspitzen

T1 Türplan 7-701
T2 Türplan 7-702
T3 Türplan 7-703
T4 Türplan 7-704
T5 Türplan 7-705
T6 Türplan 7-706
T10 Türplan 7-710
T11 Türplan 7-711
T12 Türplan 7-712
T13 Türplan 7-713


Datei: ABZ/Sihlfeld/6.23 Architekt/7_001_4_Index4 1OG.pdf

Seite, Massstab, Datum: Seite 1, 1:50, 2012 (Erneuerung, Bestand 1928)

Abgelesen: Planlegende: Neubau Betonflachdecke (Decke über EG) und Bestand Hourdisdecke (Decke über EG).

Verwendet als: Bestätigung der Deckentypen

9. Alterszentrum Abegg-Huus

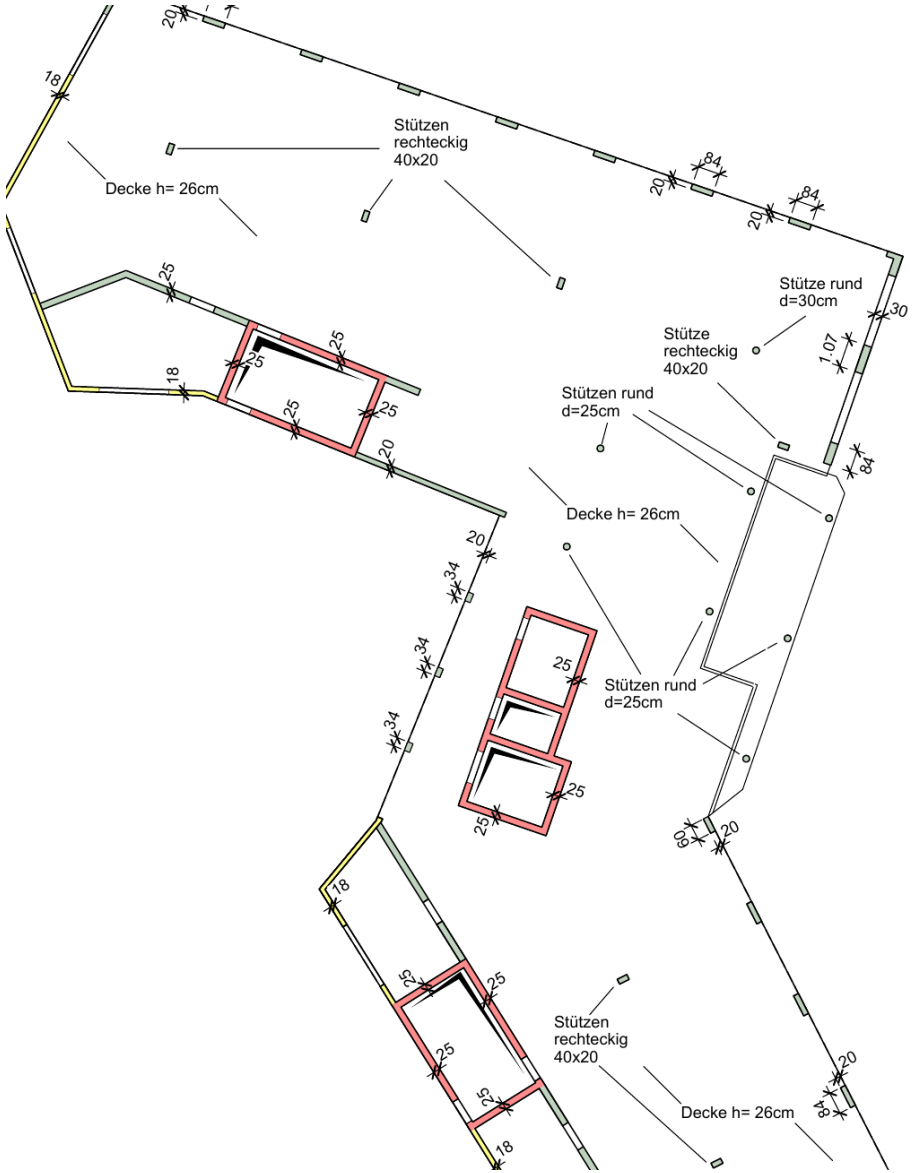


Datei:	dsp/Alterszentrum, Abegg-Huus/14729_Strukturpläne.pdf
Seite, Massstab, Datum:	Seite 5, 1:200, 2016
Abgelesen:	Strukturplan 2. OG: Decke h = 26 cm, Stützen rechteckig 40x20 cm, Stützen rund d = 25 und 30 cm, Betonwände 18...25 cm.
Verwendet als:	Deckenstärke 260 mm; eine Rasterweite ist im Plan nicht bemasst

10. Kern Süd




Datei:	dsp/Kern Süd/Tragstruktur Regelgeschoss.pdf
Seite, Massstab, Datum:	Seite 1, 1:300, 2014
Abgelesen:	Tragstruktur Regelgeschoss: Decke d = 26 cm, Stützen 25/25 cm, Fassadenpfeiler 20 cm, aussteifende Kerne 25 cm.
Verwendet als:	Deckenstärke 260 mm; Spannweiten im Massstab 1:300 nicht belegbar


11. Lagerplatz

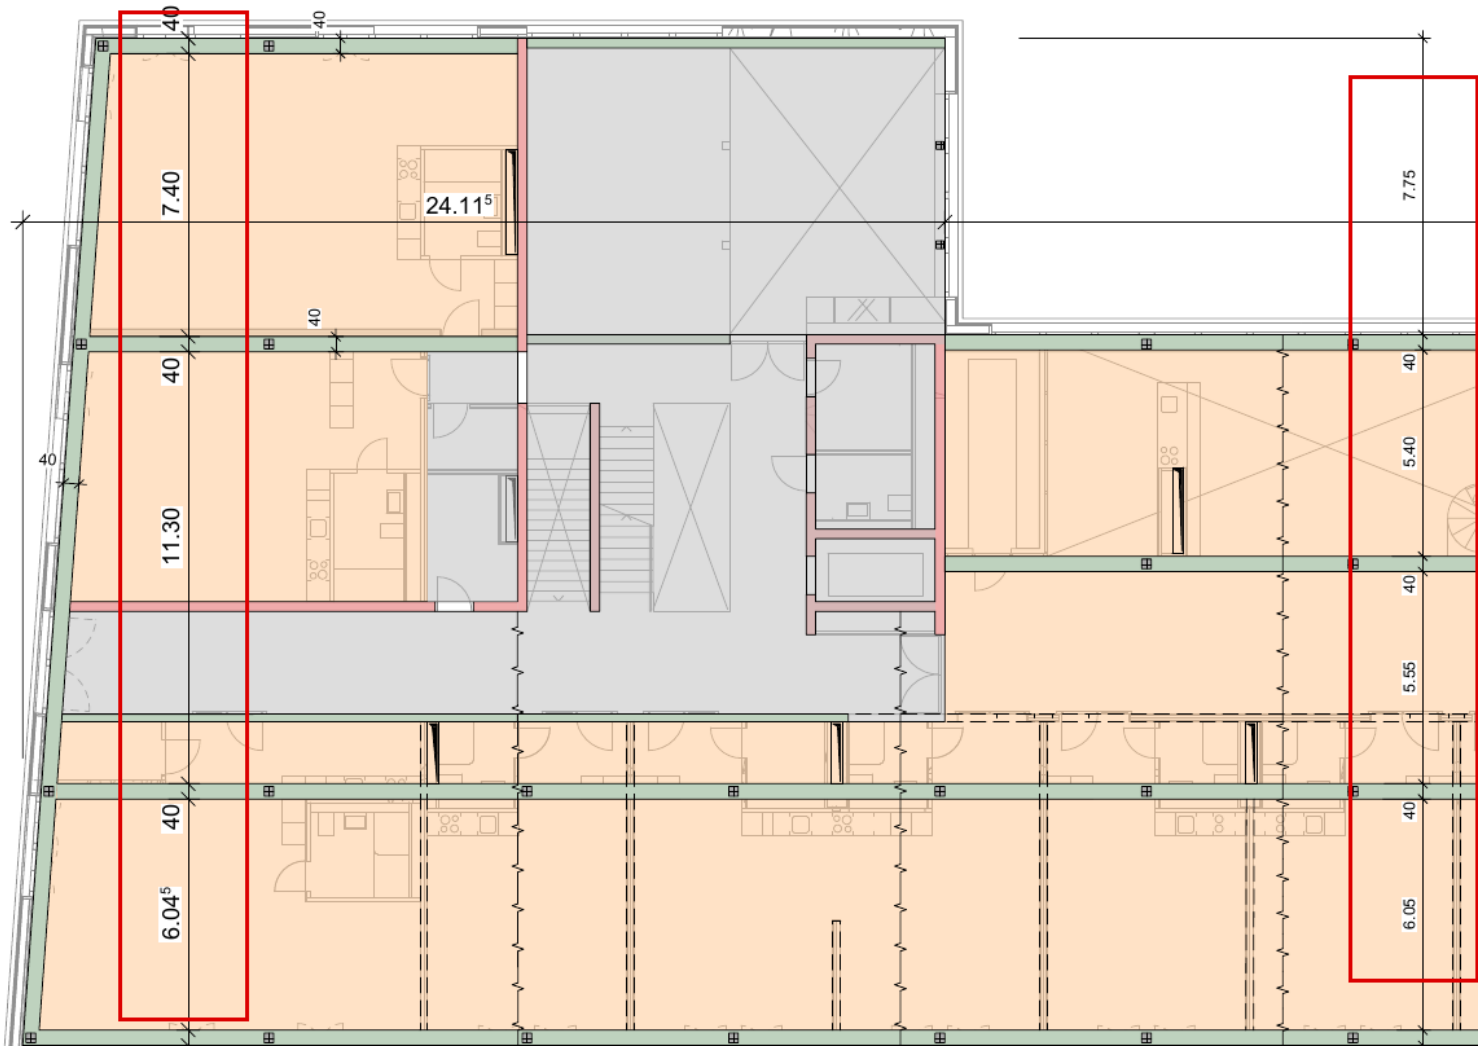

Datei:	dsp/Lagerplatz/141_B_S_01-05_M20_32_V Verbunddecke Referenzgeschoss.pdf
Seite, Massstab, Datum:	Seite 1, 1:200, 2016
Abgelesen:	Grundriss 2. OG: Spannweiten der Verbunddecke zwischen den Unterzügen 7.40 / 11.30 / 6.04 m im Kopfbau und 7.75 / 5.40 / 5.55 / 6.05 m im Regelbereich.
Verwendet als:	massgebende Spannweite 6.05 m (grösster Wert des Regelbereichs; welcher Wert die Spannweite der Verbunddecke und welcher jene der Unterzüge ist, geht aus dem Plan nicht hervor)

12. Lagerplatz

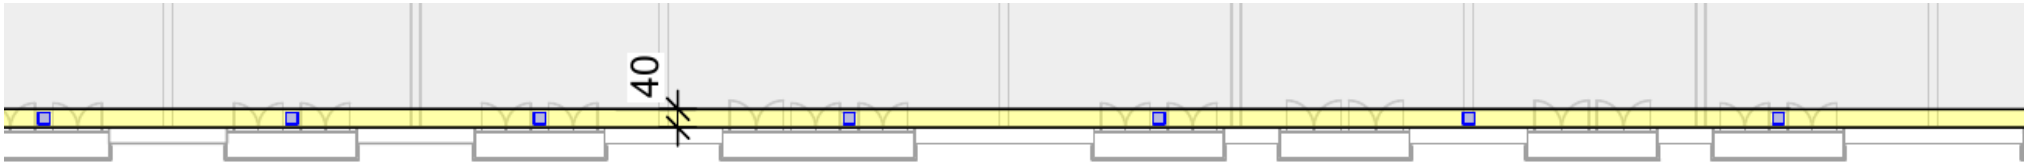

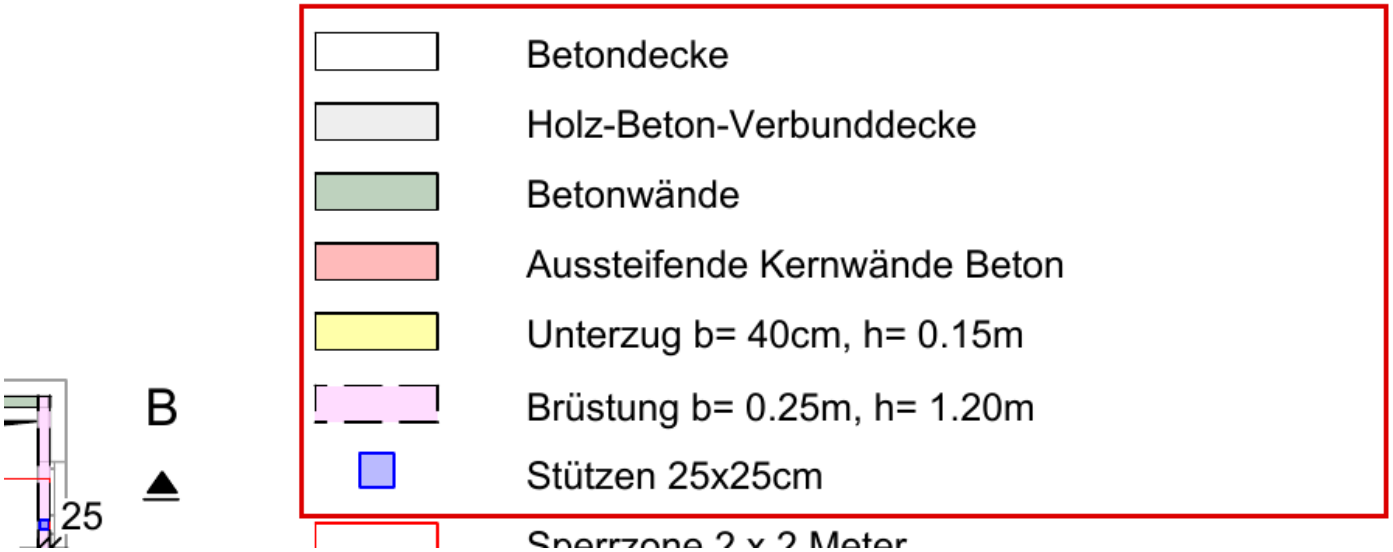

Datei:	dsp/Lagerplatz/14713-104 1. Obergeschoss, 2.Obergeschoss.pdf
Seite, Massstab, Datum:	Seite 1, Legende, 2016
Abgelesen:	Legende: Holz-Beton-Verbunddecke, Unterzug b = 40 cm, h = 0.15 m, Brüstung b = 0.25 m, h = 1.20 m, Stützen 25x25 cm.
Verwendet als:	Unterzugsgeometrie 40 x 15 cm unter der Platte