


Einfeldträger vs. Durchlaufträger (3-8m)

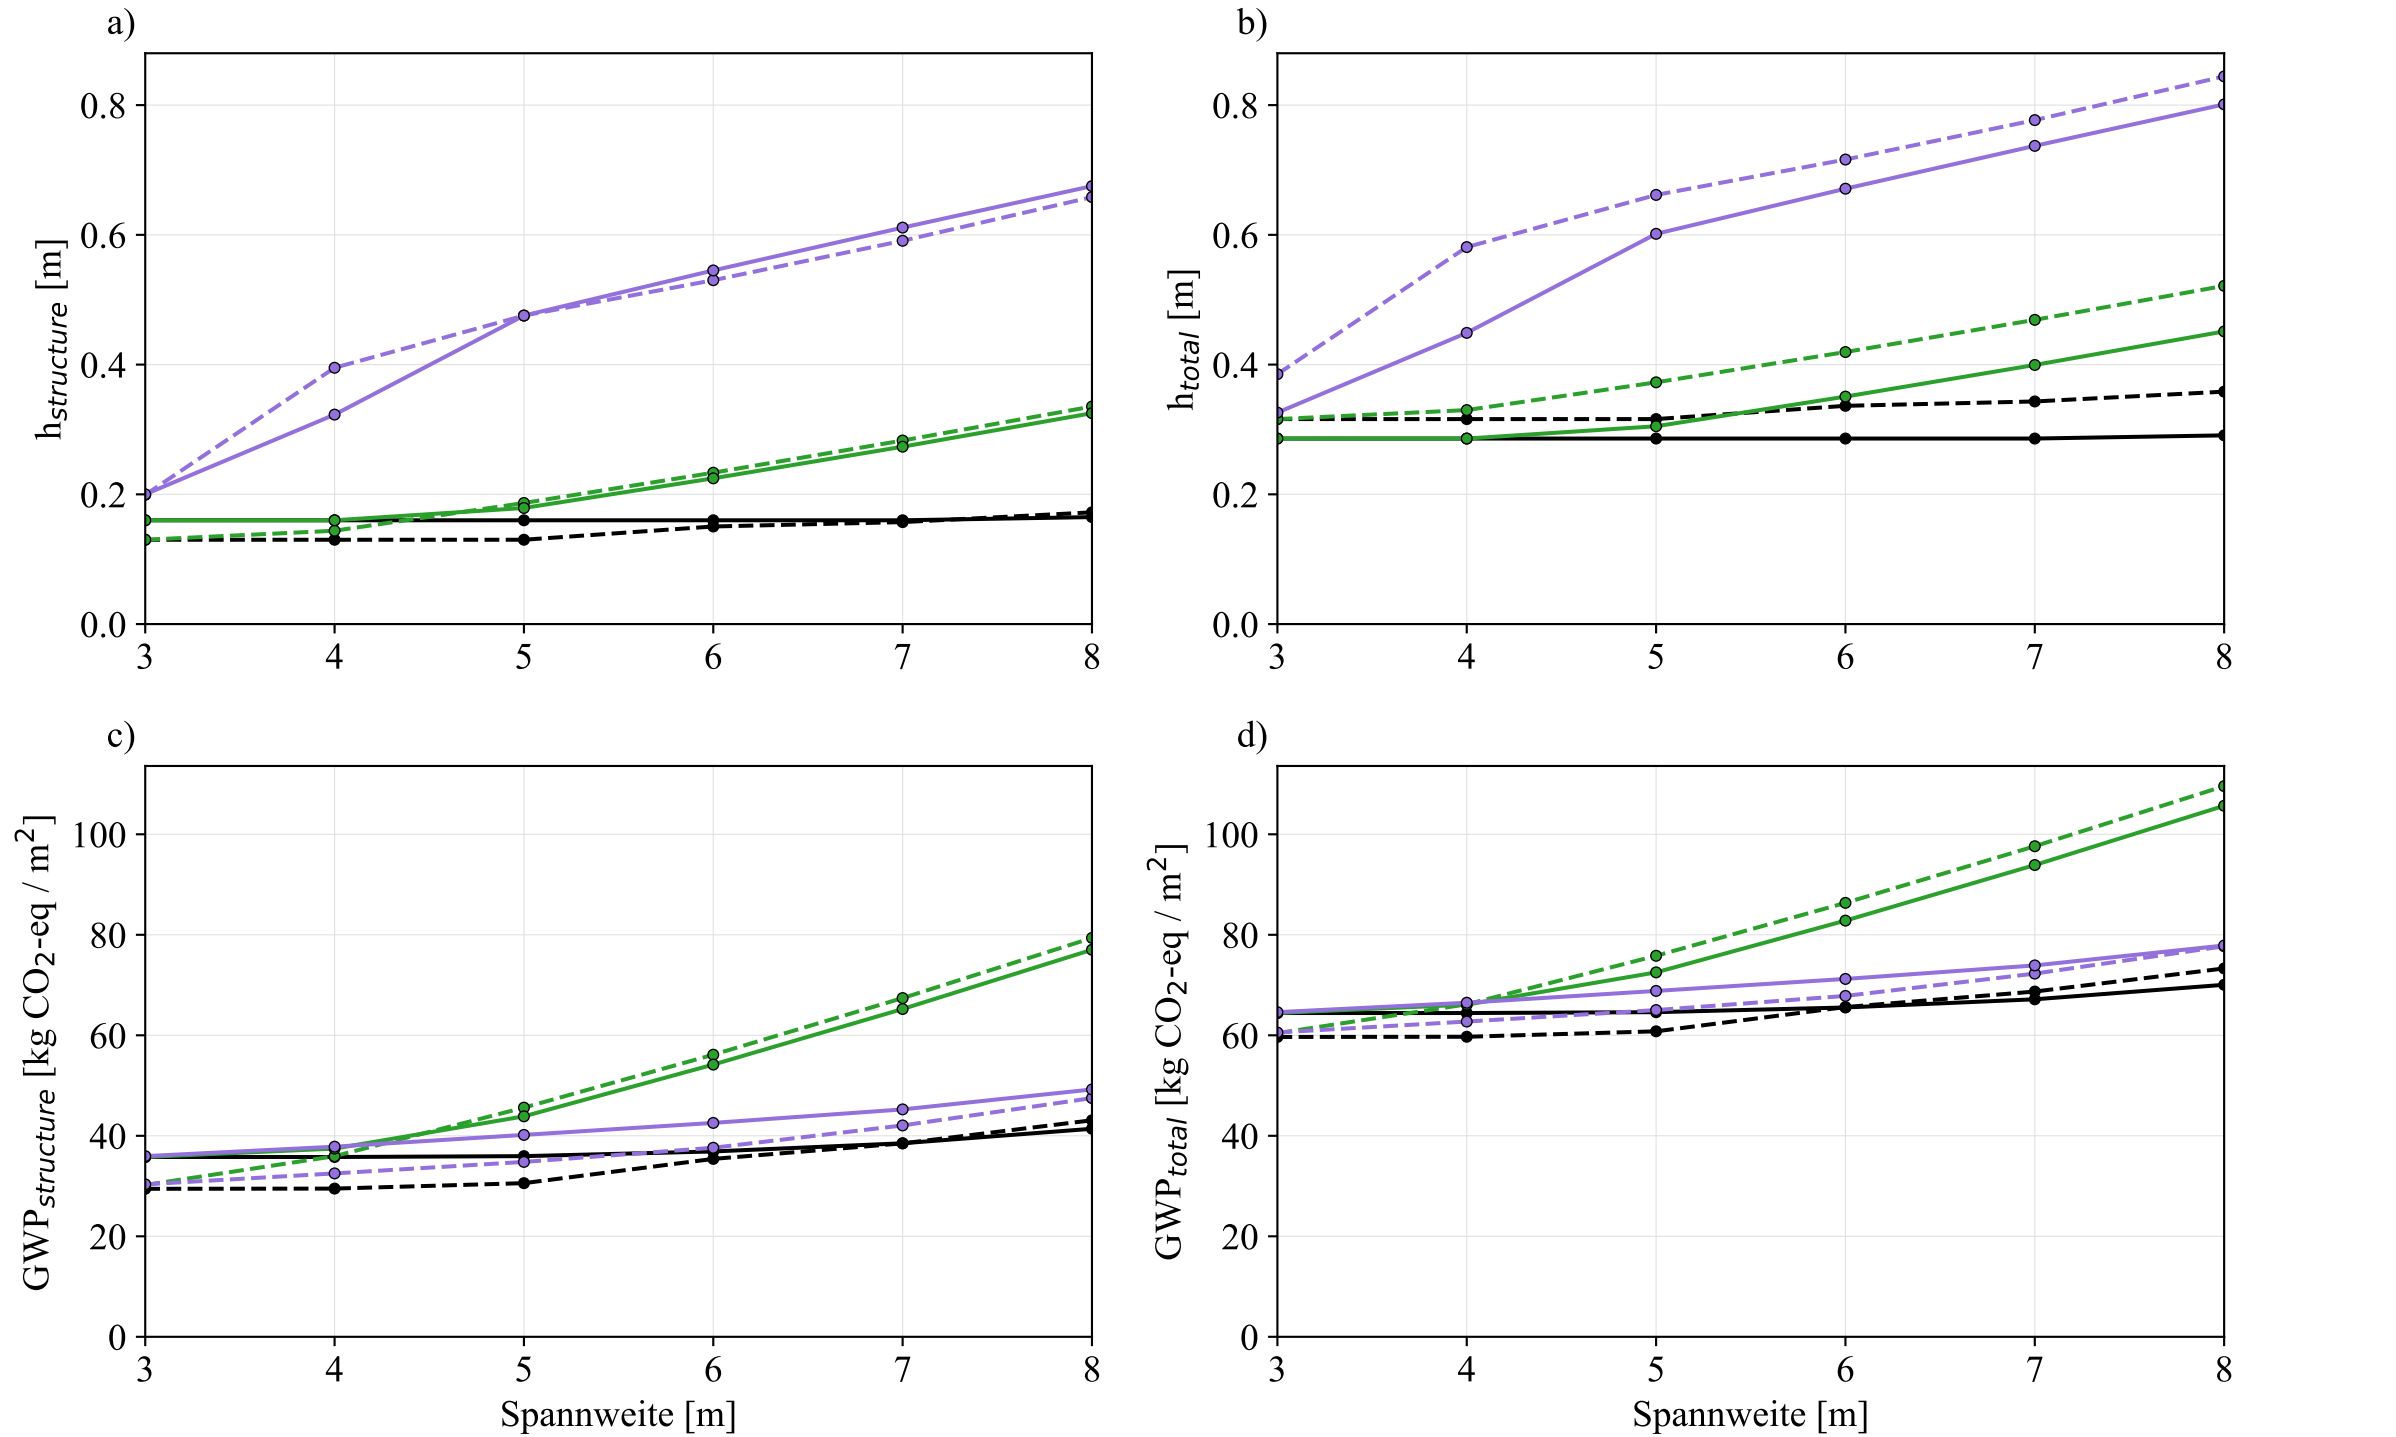

- | | | | | | |
|--|---|--|---|--|---|
| | Vollplatte, einachsrig tragend, durchlaufend (Standardaufbau) | | Vollplatte, einachsrig tragend, einfach gelagert (Standardaufbau) | | Rippenplatte, einachsrig tragend, einfach gelagert (Standardaufbau) |
| | Vollplatte, einachsrig tragend, durchlaufend (Standardaufbau + Schüttung) | | Vollplatte, einachsrig tragend, einfach gelagert (Standardaufbau + Schüttung) | | Rippenplatte, einachsrig tragend, einfach gelagert (Standardaufbau + Schüttung) |