


Plattensysteme vs. Durchlaufträger (3-12m)

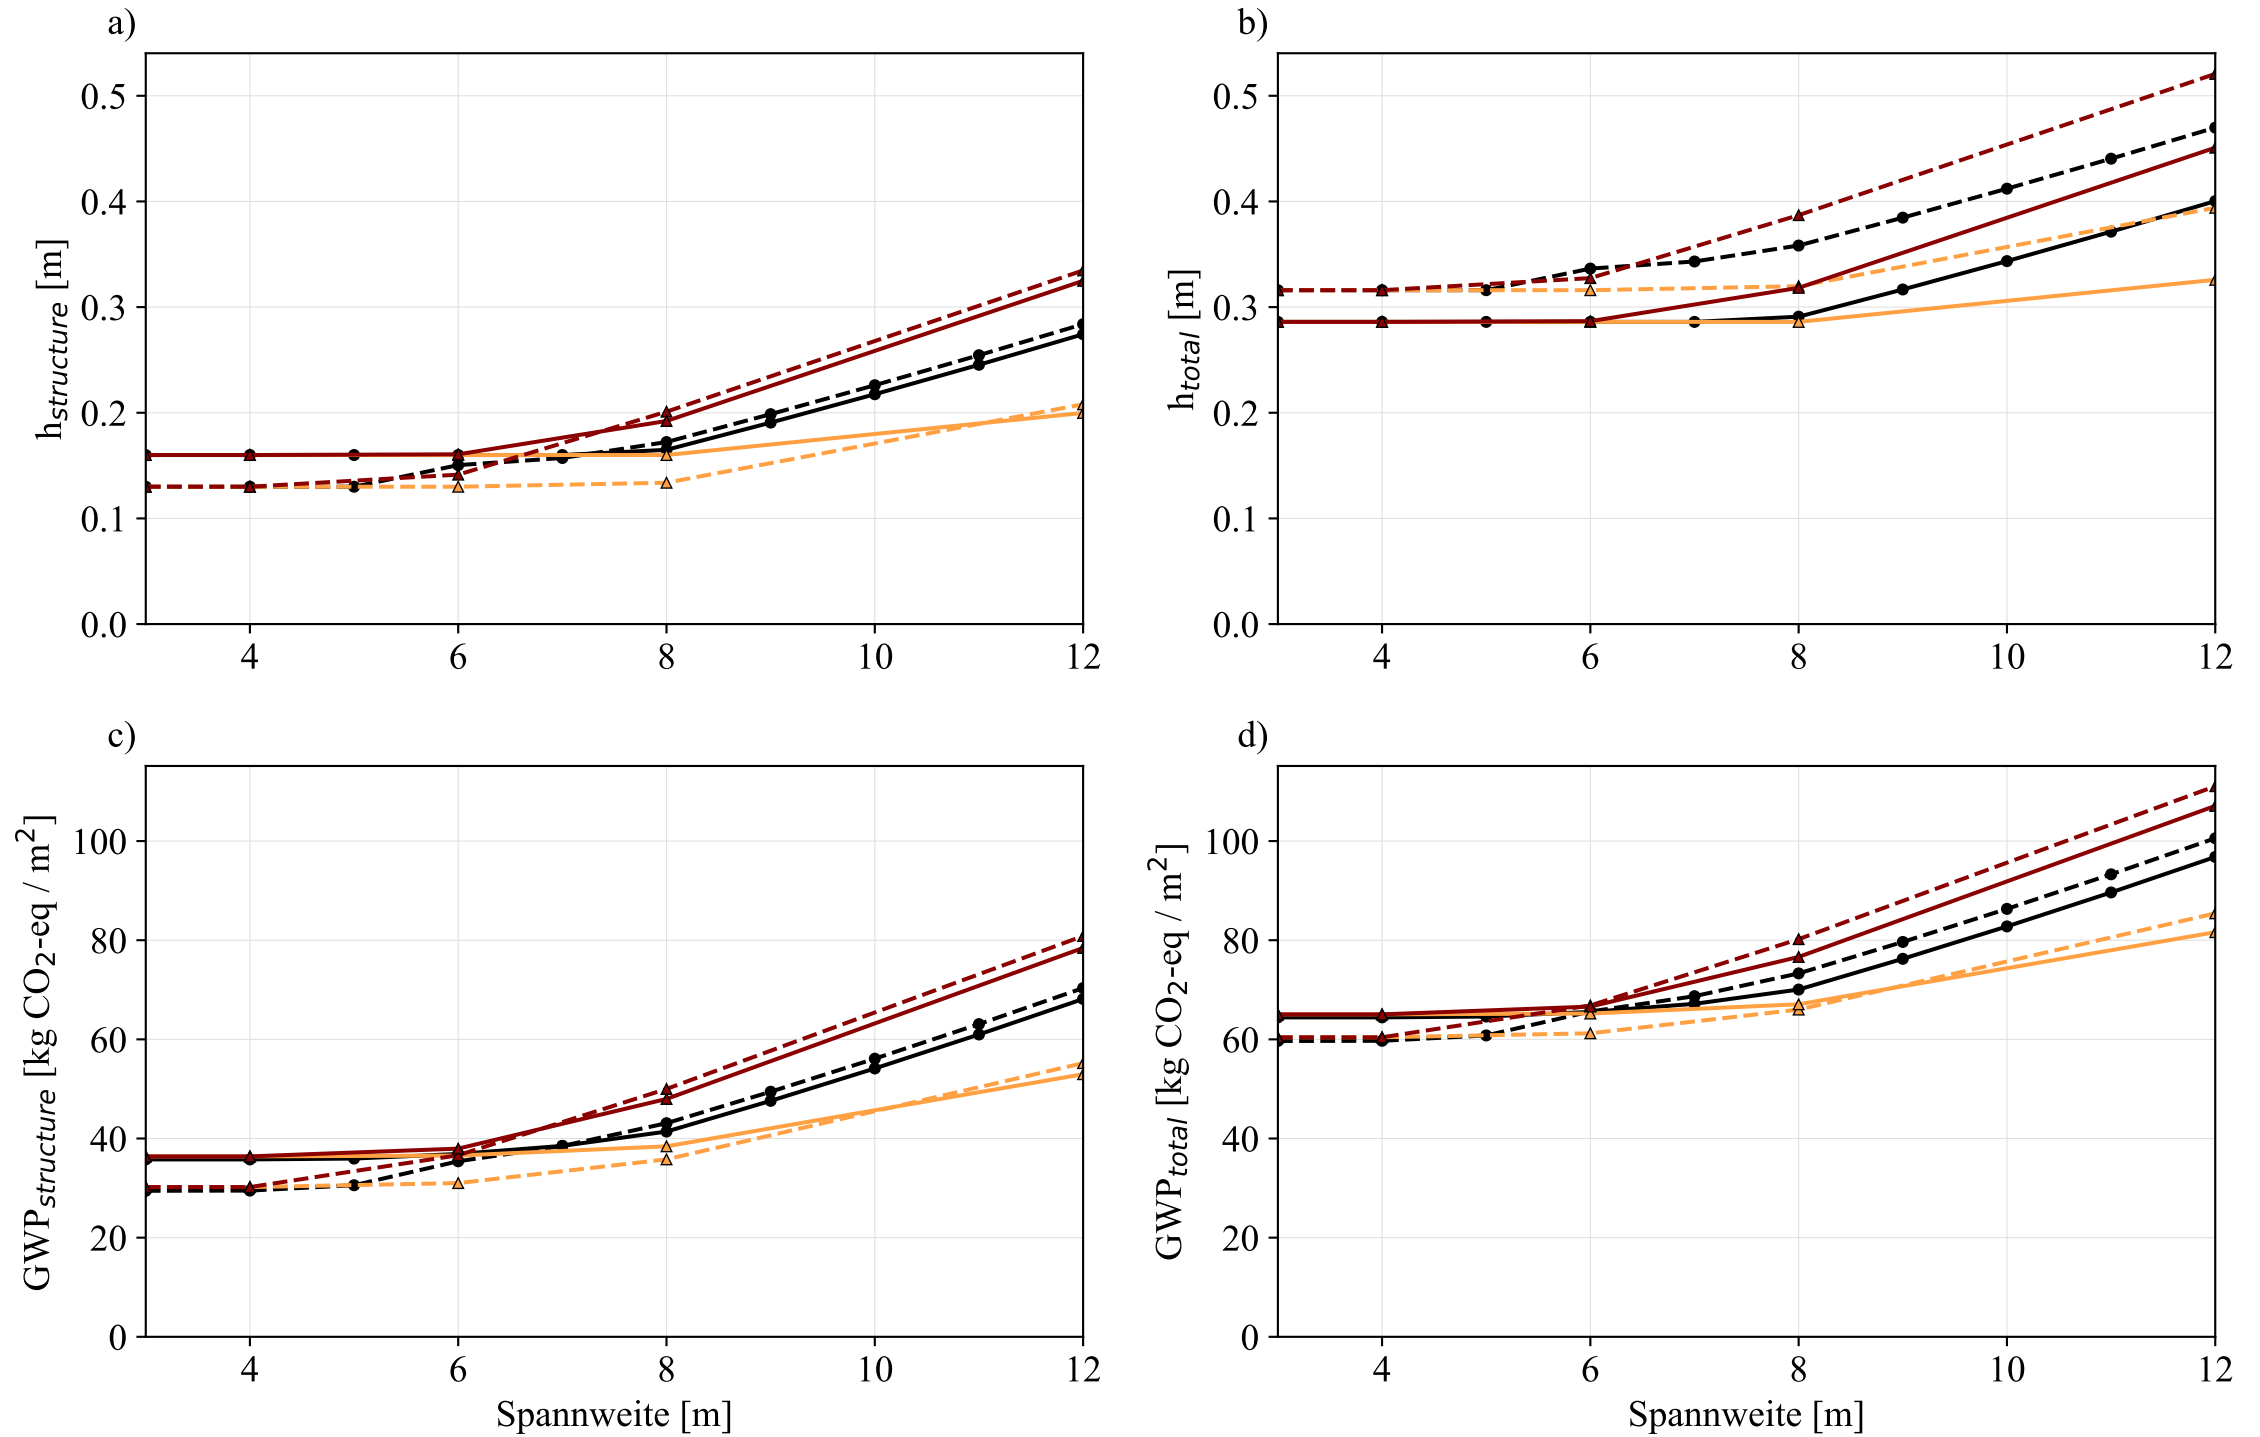

- | | | | | | |
|---------|---|---------|--|---------|--|
| —●— | Vollplatte, einachsrig tragend, durchlaufend (Standardaufbau) | —▲— | Vollplatte, zweiachsrig tragend, durchlaufend (Standardaufbau) | —▲— | Vollplatte, zweiachsrig tragend, einfach gelagert (Standardaufbau) |
| - -●- - | Vollplatte, einachsrig tragend, durchlaufend (Standardaufbau + Schüttung) | - -▲- - | Vollplatte, zweiachsrig tragend, durchlaufend (Standardaufbau + Schüttung) | - -▲- - | Vollplatte, zweiachsrig tragend, einfach gelagert (Standardaufbau + Schüttung) |