


Höhe Struktur h_{struc} für Systeme mit Standardbodenaufbau

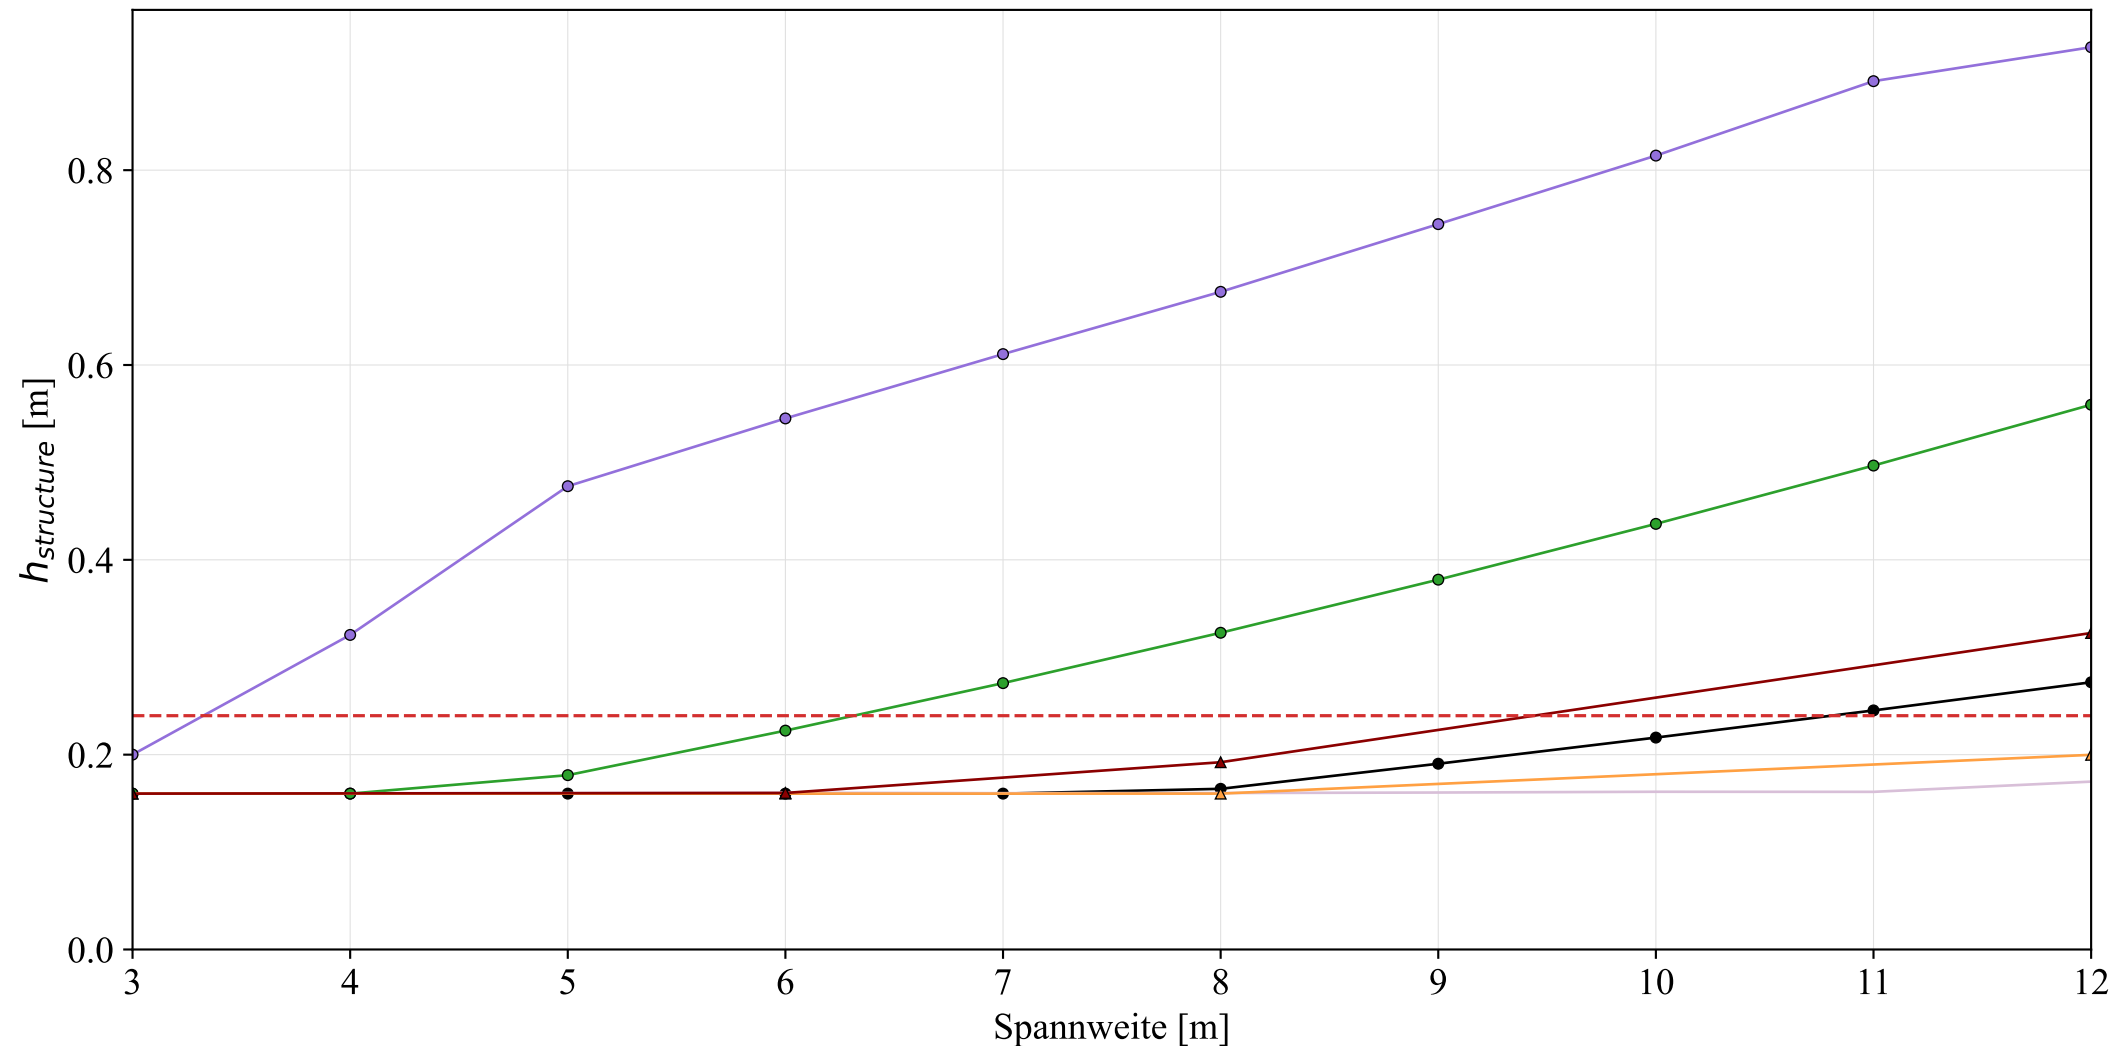

- Plattenstreifen, eingespannt (Standardaufbau)
- Plattenstreifen, frei aufgelegt (Standardaufbau)
- Mindeststärke Schallschutz für erhöhte Anforderungen (24 cm)
- Platte liniengelagert, eingespannt (Standardaufbau)
- Platte liniengelagert, frei aufgelegt (Standardaufbau)
- Plattenbalken, frei aufgelegt (Standardaufbau)
- Plattenbalken, frei aufgelegt (Standardaufbau), Flanshhöhe