


Höhe Struktur h_{struc} für Systeme mit Standardbodenaufbau

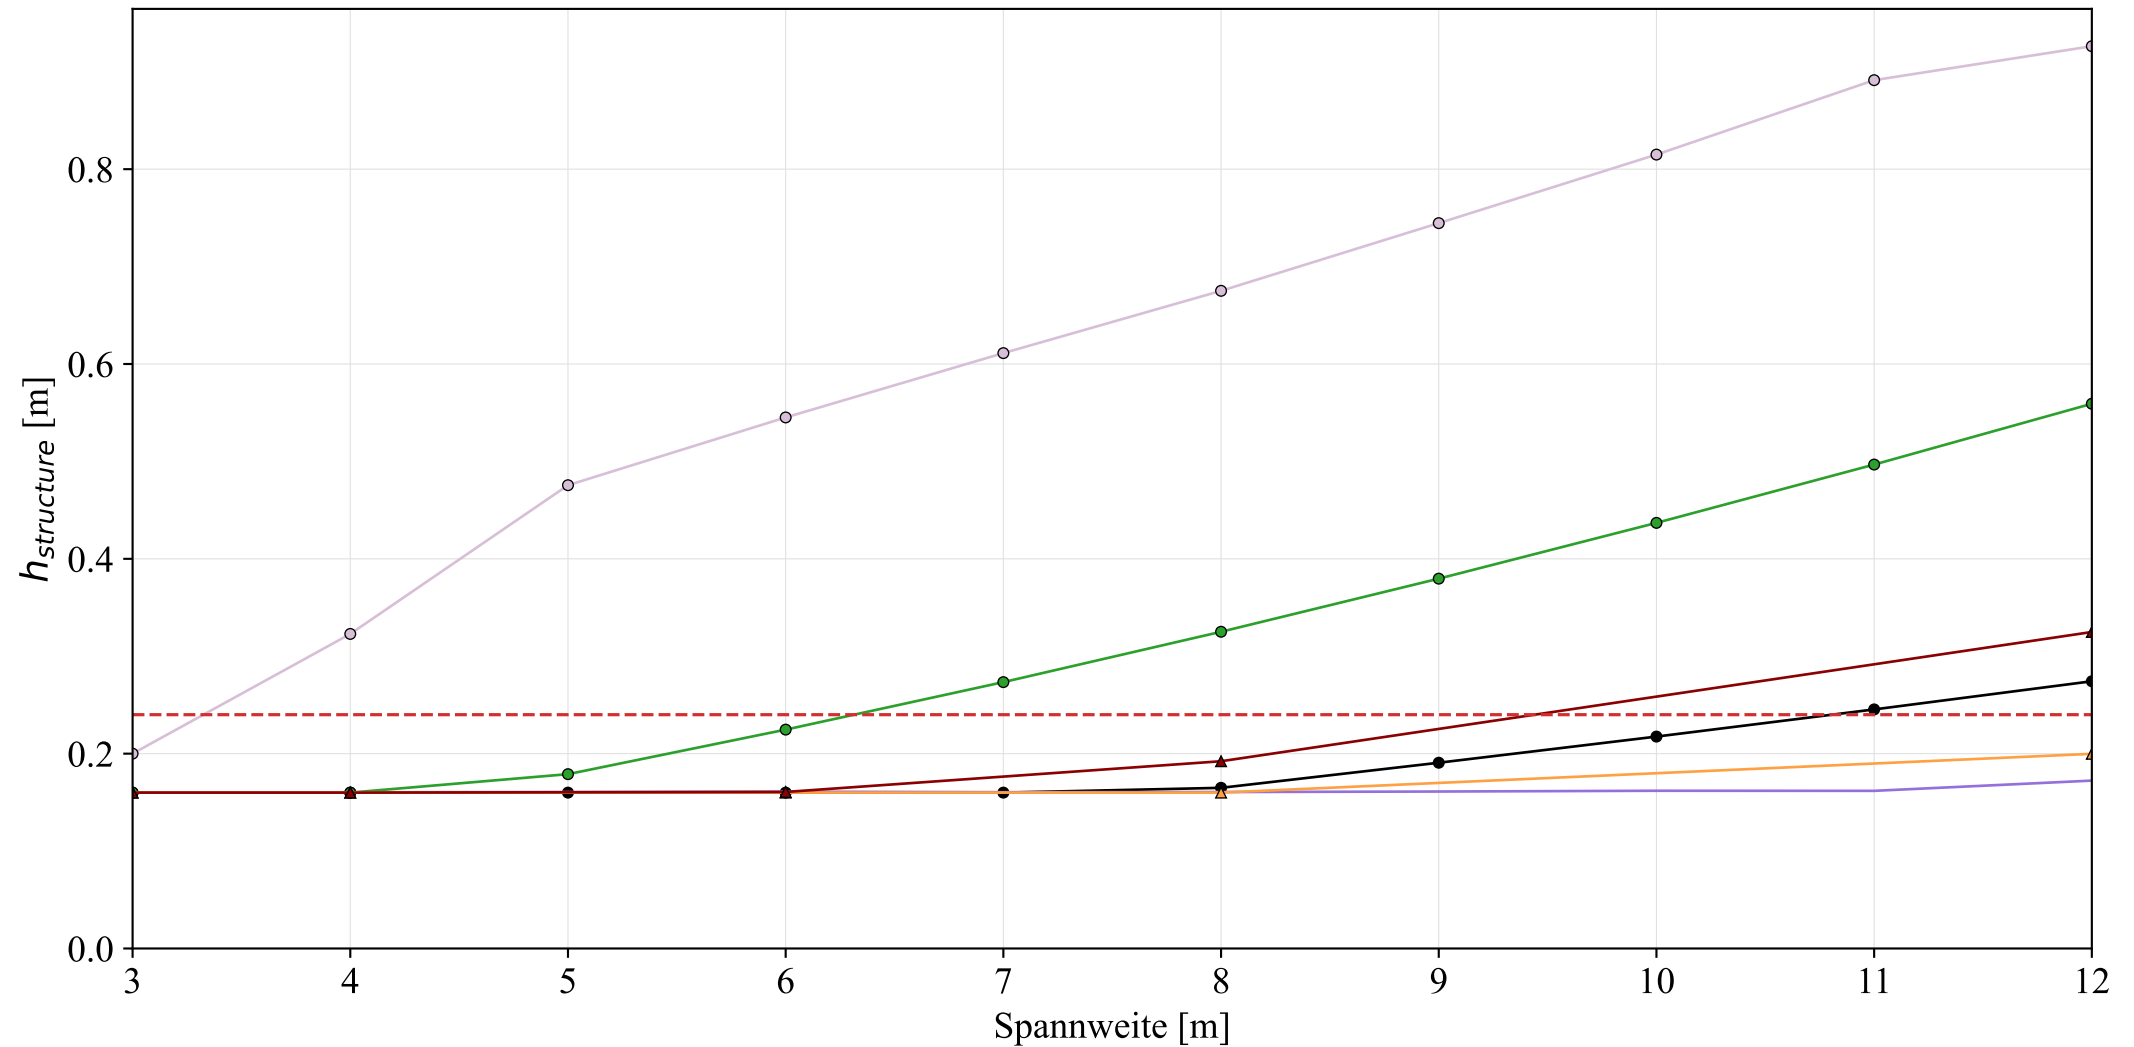

- Vollplatte, einachsrig tragend, einfach gelagert (Standardaufbau)
- Vollplatte, einachsrig tragend, durchlaufend (Standardaufbau)
- ▲— Vollplatte, zweiachsrig tragend, einfach gelagert (Standardaufbau)
- ▲— Vollplatte, zweiachsrig tragend, durchlaufend (Standardaufbau)
- Rippenplatte, einachsrig tragend, einfach gelagert (Standardaufbau)
- Rippenplatte, einachsrig tragend, einfach gelagert (Standardaufbau), Flanschhöhe
- - - Mindeststärke für erhöhte Schallschutzanforderungen (24 cm)