


Höhe Struktur h_{struc} für Systeme mit Standardbodenaufbau

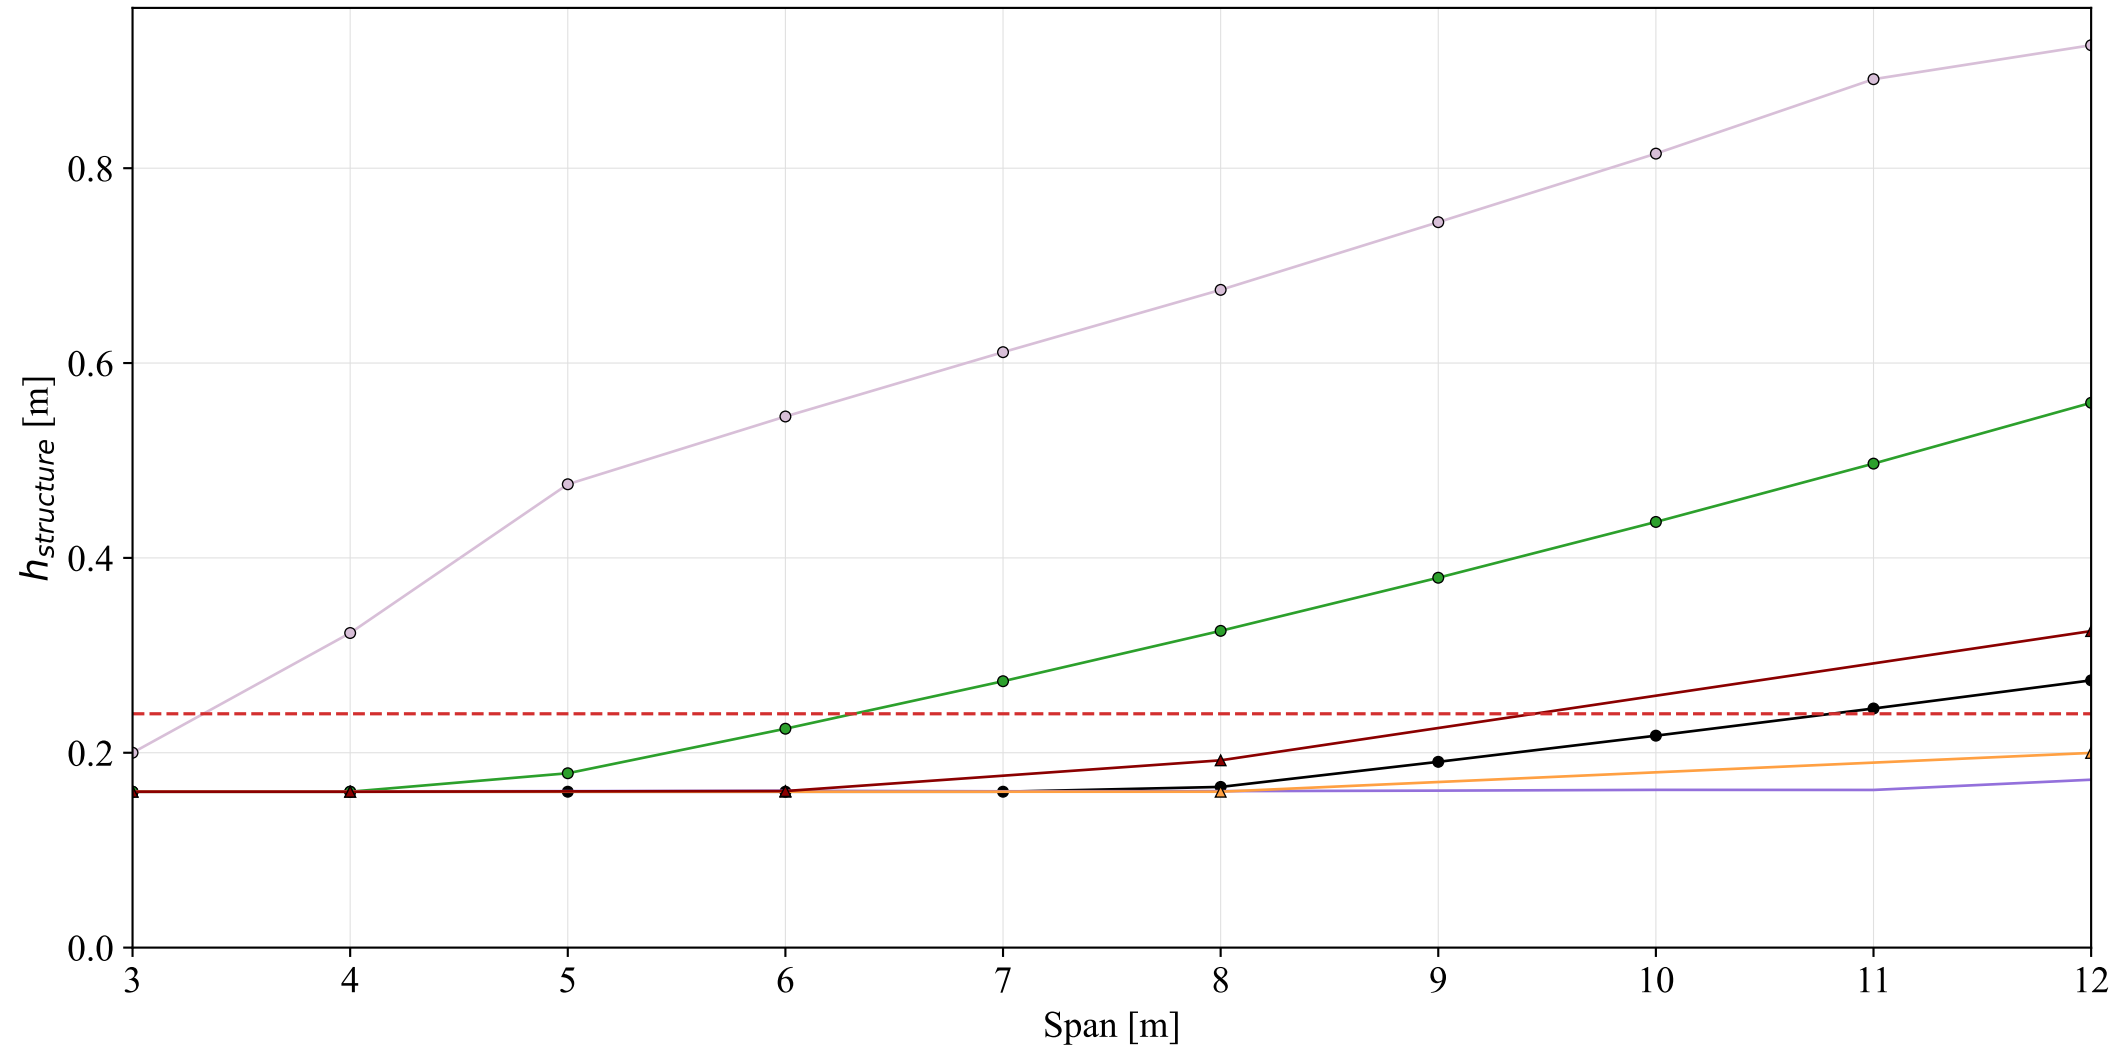

—●— Solid slab, single-axis load-bearing, simply supported (standard superstructure)

—●— Solid slab, single-axis load-bearing, continuous (standard superstructure)

--- construction height to meet higher sound insulation requirements (24 cm)

—▲— Solid slab, two-axis load-bearing, simply supported (standard superstructure)

—▲— Solid slab, two-axis load-bearing, continuous (standard superstructure)

—○— Ribbed plate, single-axis load-bearing, simply supported, (standard superstructure)

— Ribbed plate, single-axis load-bearing, simply supported, (standard superstructure), flange height