


Höhe Struktur h_{struc} für Systeme mit Standardbodenaufbau

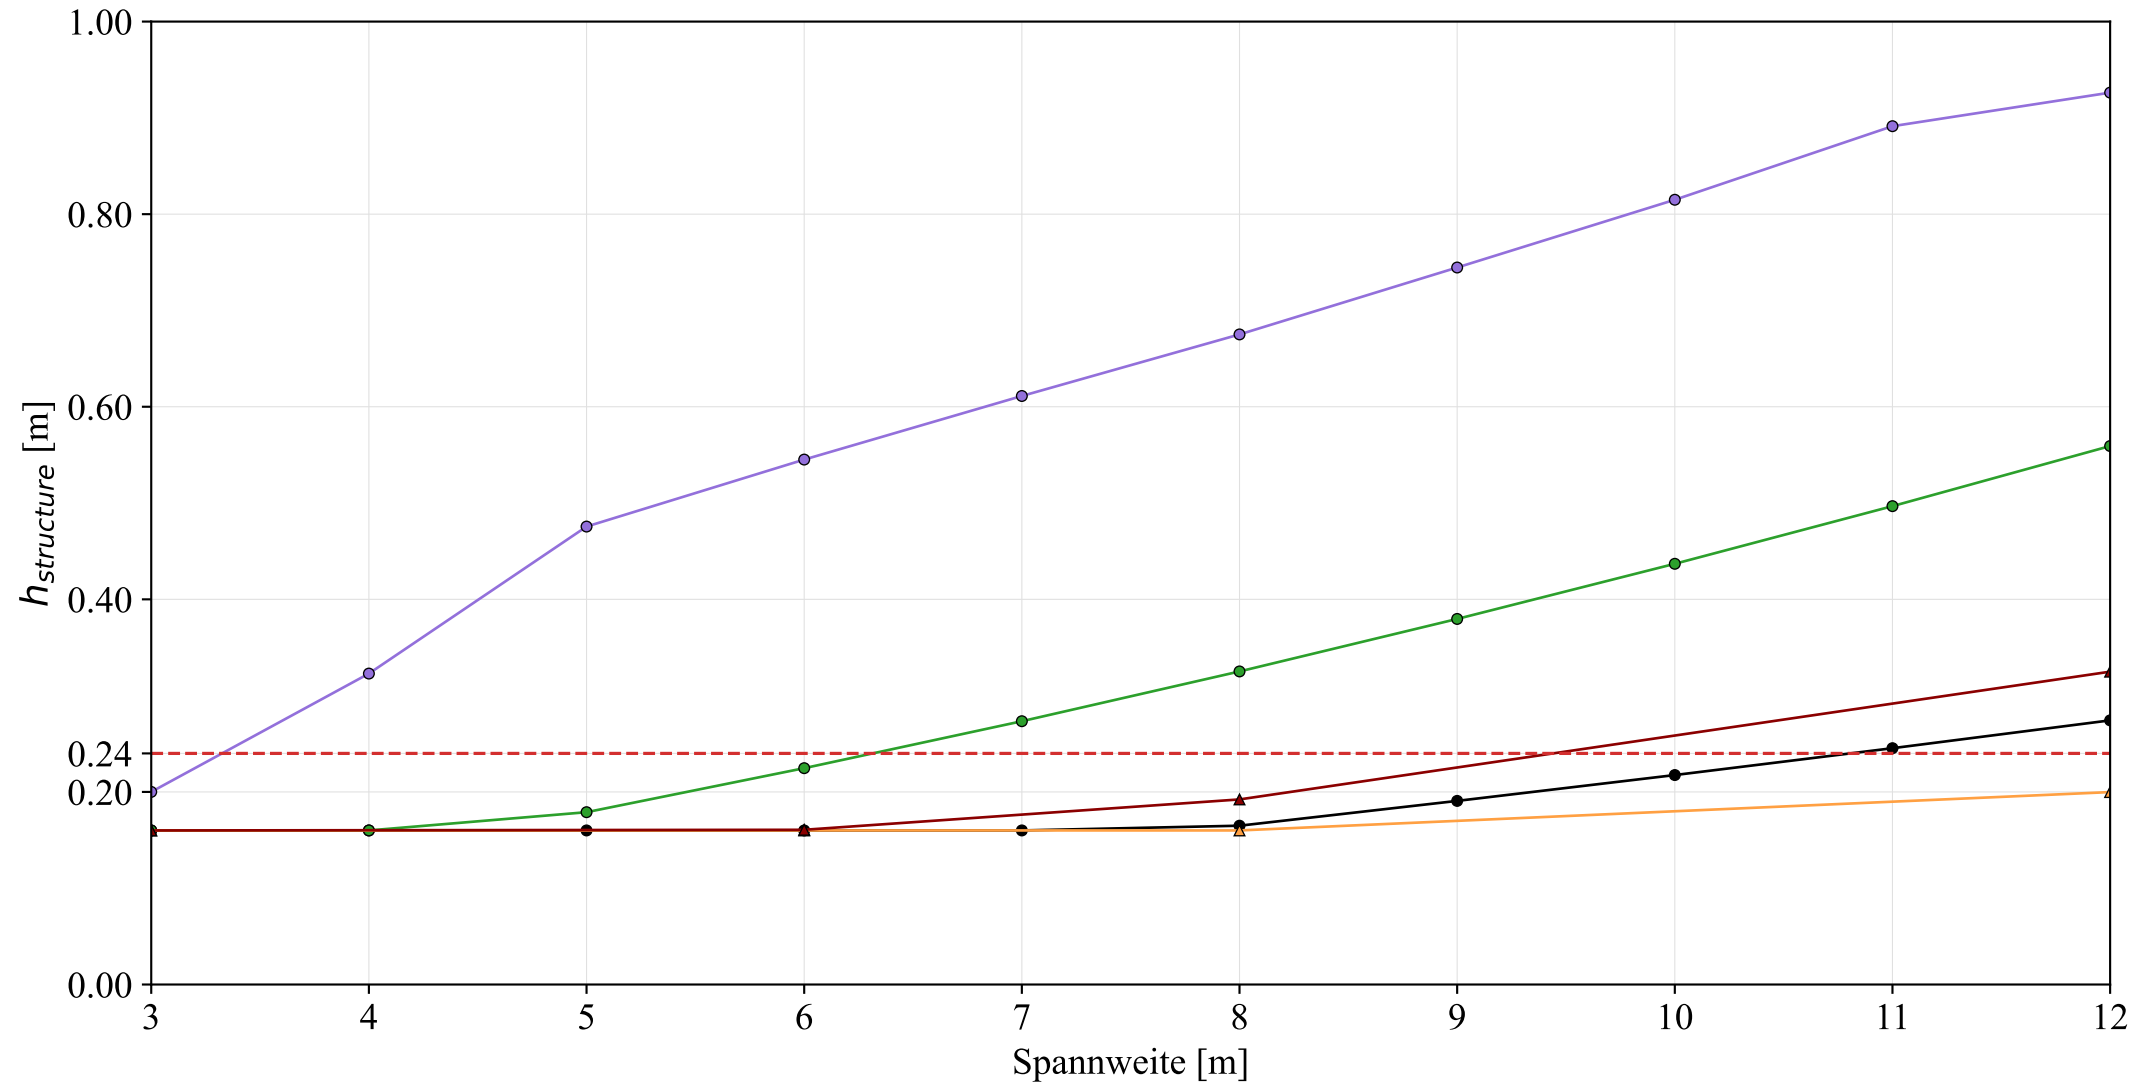

—●— Plattenstreifen, eingespannt
(Standardaufbau)

—▲— Platte liniengelagert, eingespannt
(Standardaufbau)

—●— Plattenbalken, frei aufgelegt
(Standardaufbau)

—●— Plattenstreifen, frei aufgelegt
(Standardaufbau)

—▲— Platte liniengelagert, frei aufgelegt
(Standardaufbau)

- - - Mindeststärke Schallschutz für erhöhte
Anforderungen (24 cm)